

P R E F L E X  
b u i l d i n g

## MINI CABIN



P R E F L E X O F F I C E

No.	Description	Date

## Assamble

Project number 001

Date Issue Date


Drawn by Author

Checked by Checker


A100

Scale

08/06/2021 08:26:48 a.m.

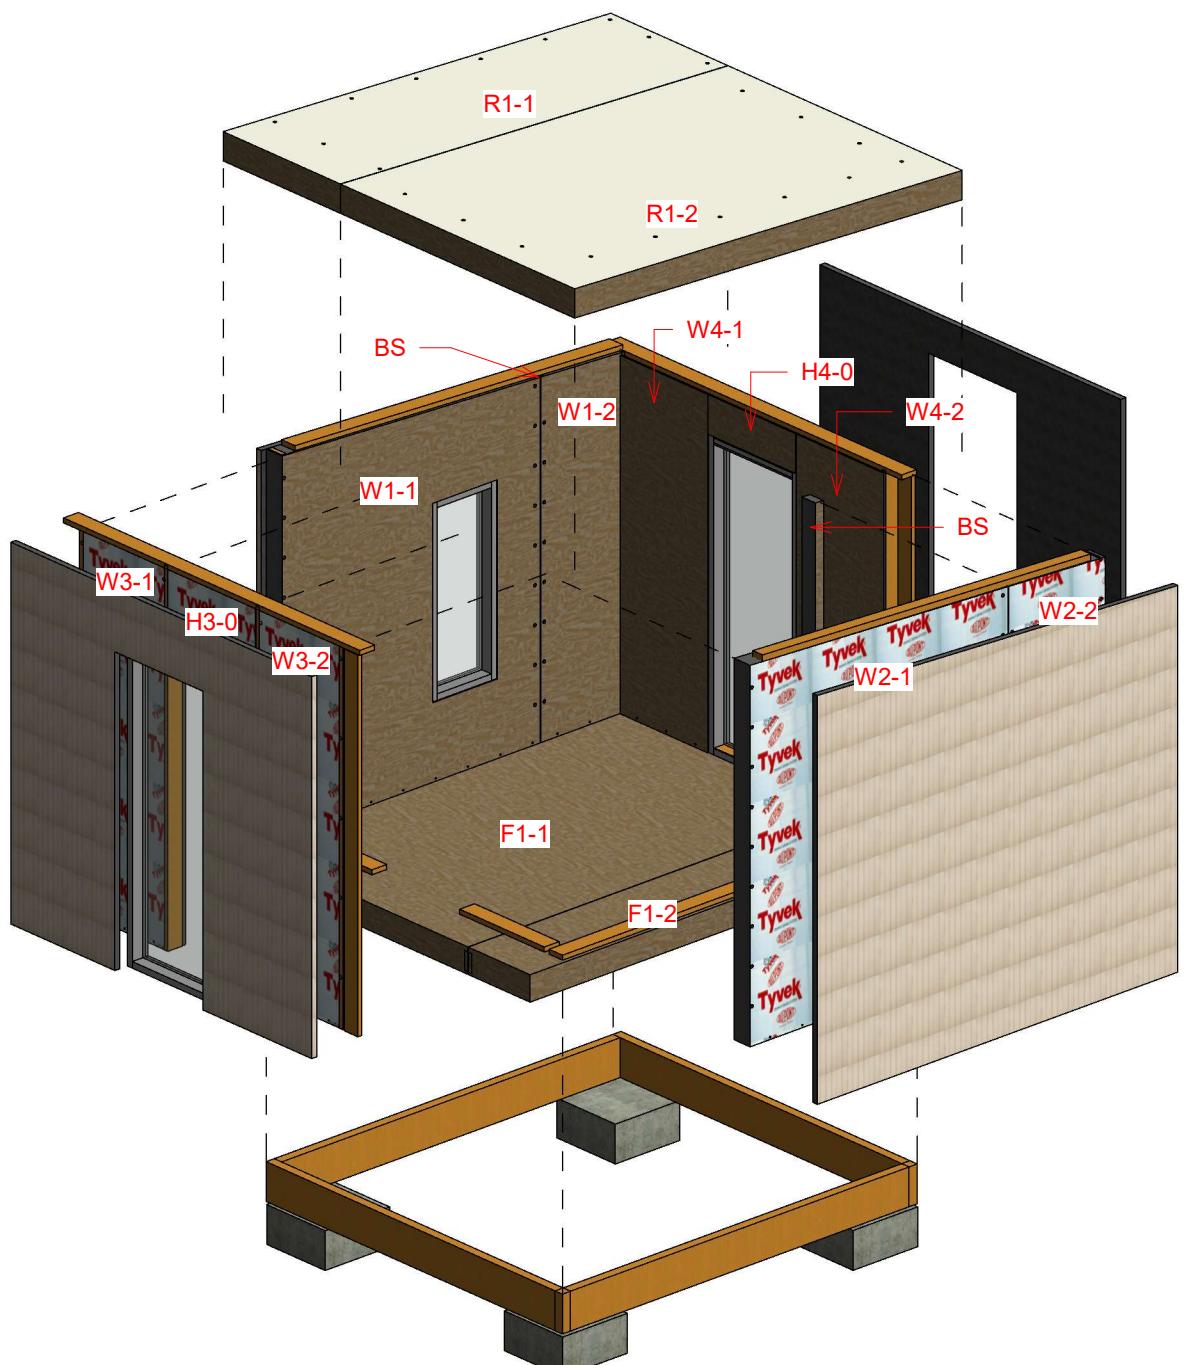


1 Assemble

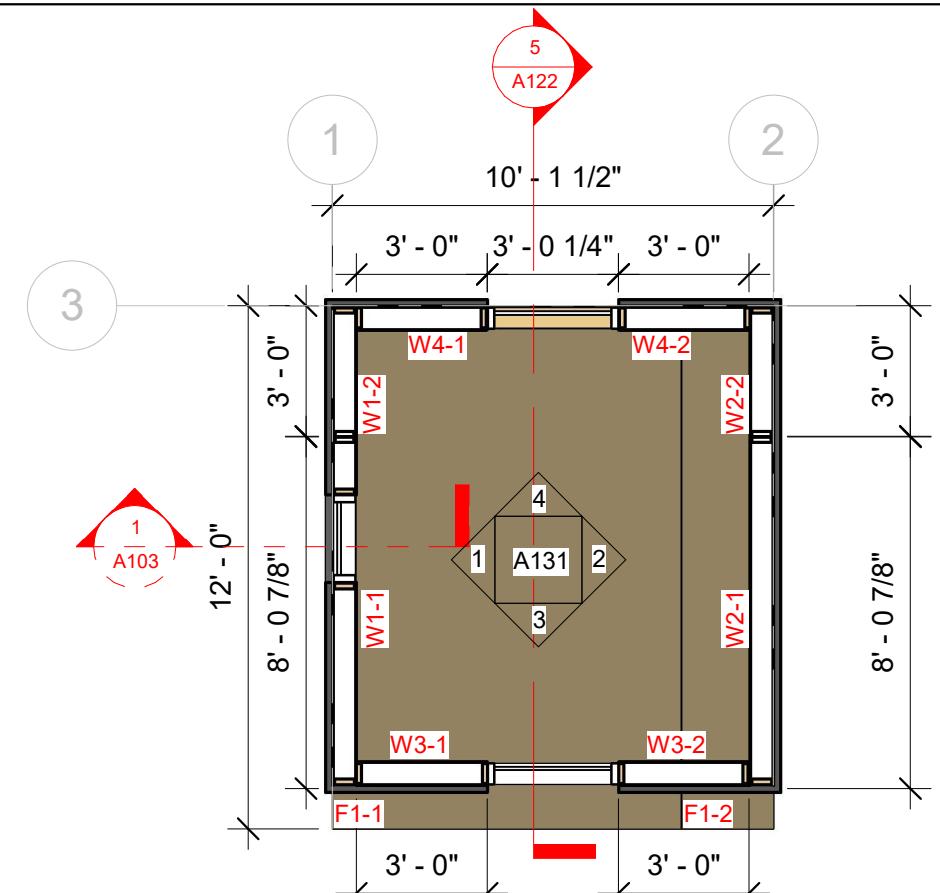


**Level 1**  
1/4" = 1'-0"



FLOOR FINISHED PROPOSED

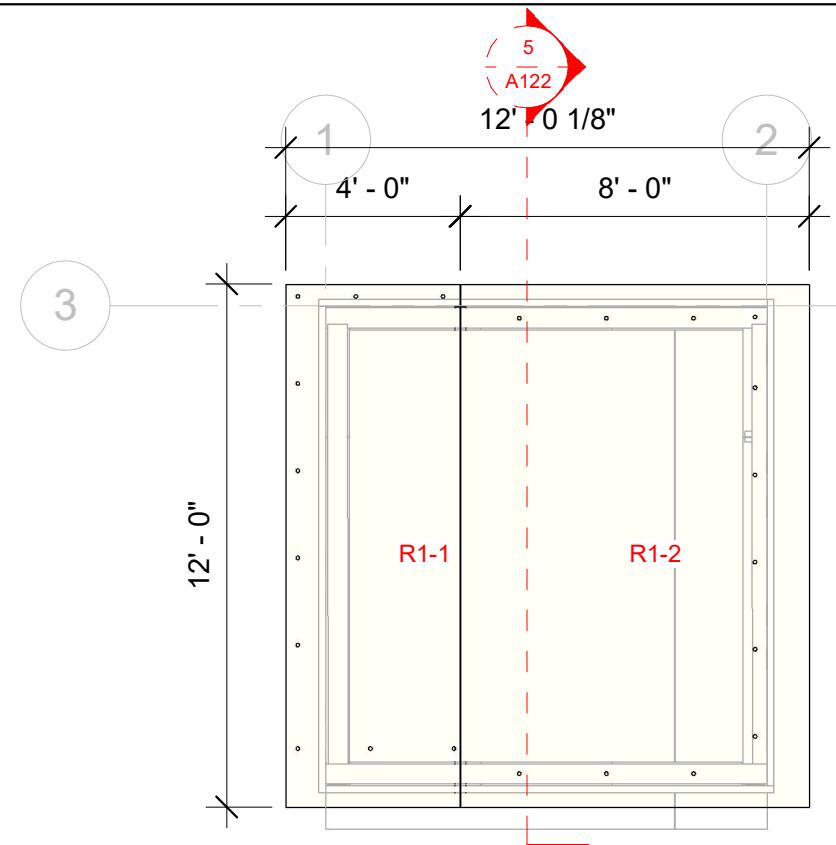


**Level 2**  
1/4" = 1'-0"

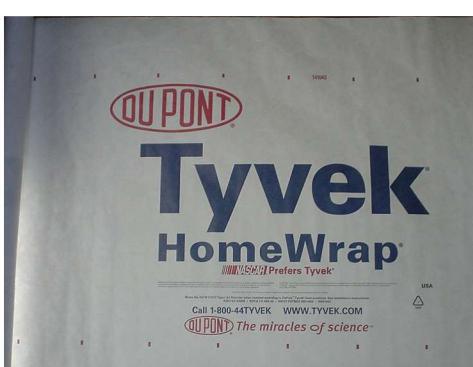


\$ 0.97 Dls SQFT

WALLS FINISHED PROPOSED

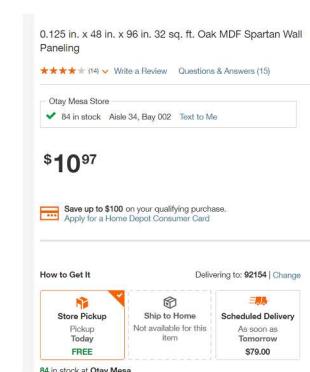

Scale  
1/4" = 1'-0"

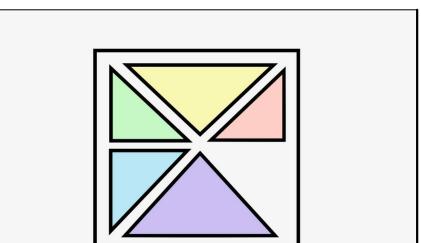

## MINI CABIN



### PREFLEX OFFICE

No.	Description	Date

### Plan and Roof

Project number  
001


Date  
Issue Date

Drawn by  
Author

Checked by  
Checker

A101

08/06/2021 08:26:49 a.m.

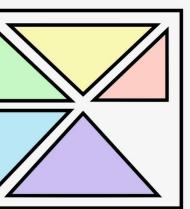

P R E F L E X  
b u i l d i n g

## MINI CABIN



P R E F L E X O F F I C E

No.	Description	Date

## Elevations

Project number 001

Date Issue Date





Drawn by Author


Checked by Checker

A102

Scale 1/4" = 1'-0"

08/06/2021 08:26:51 a.m.

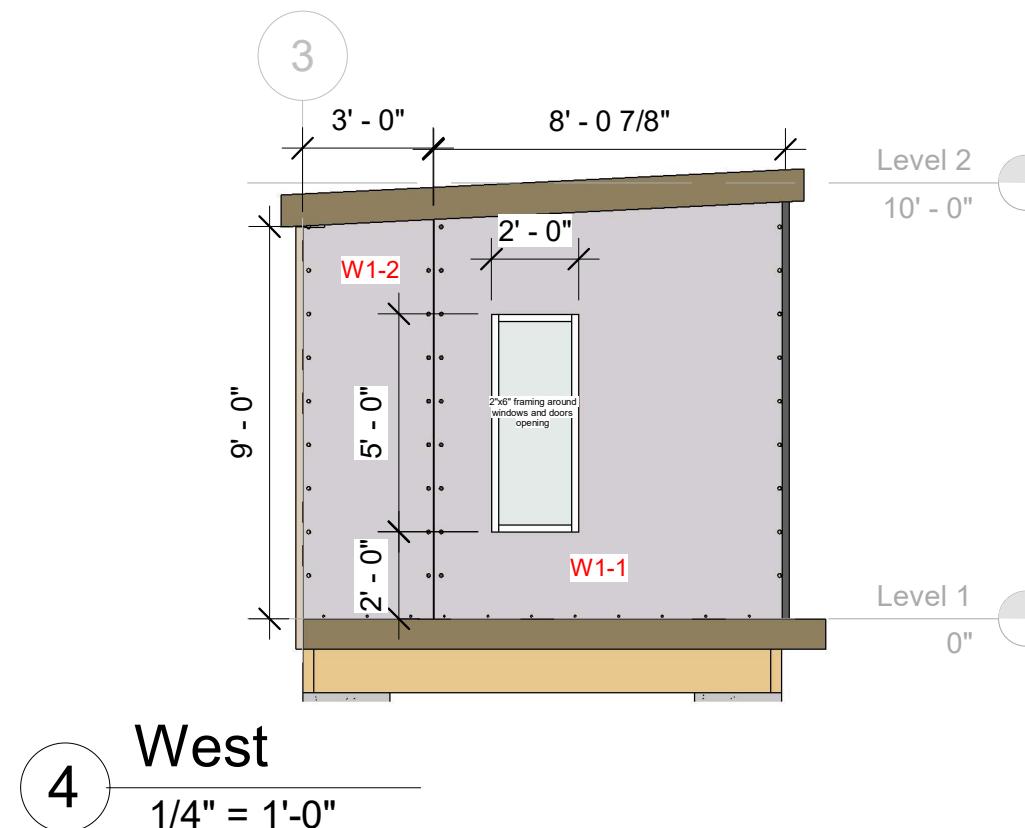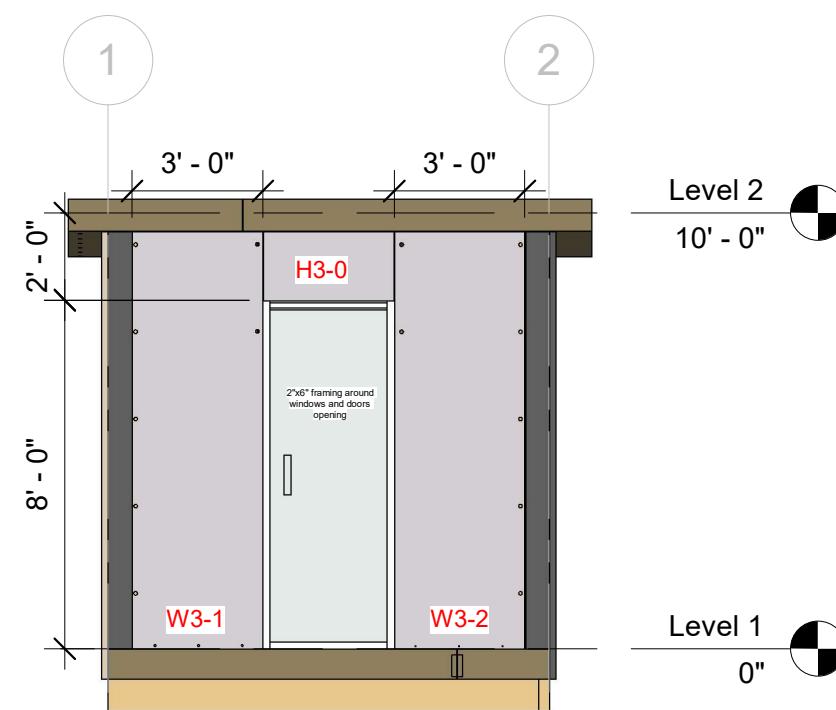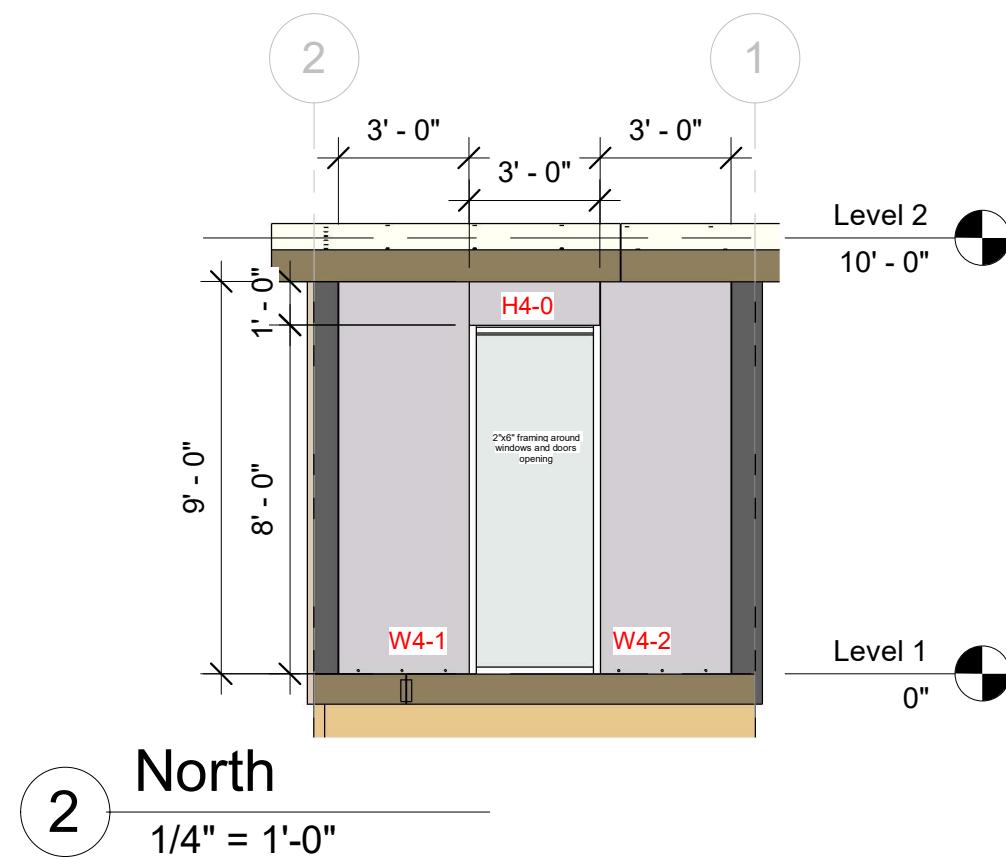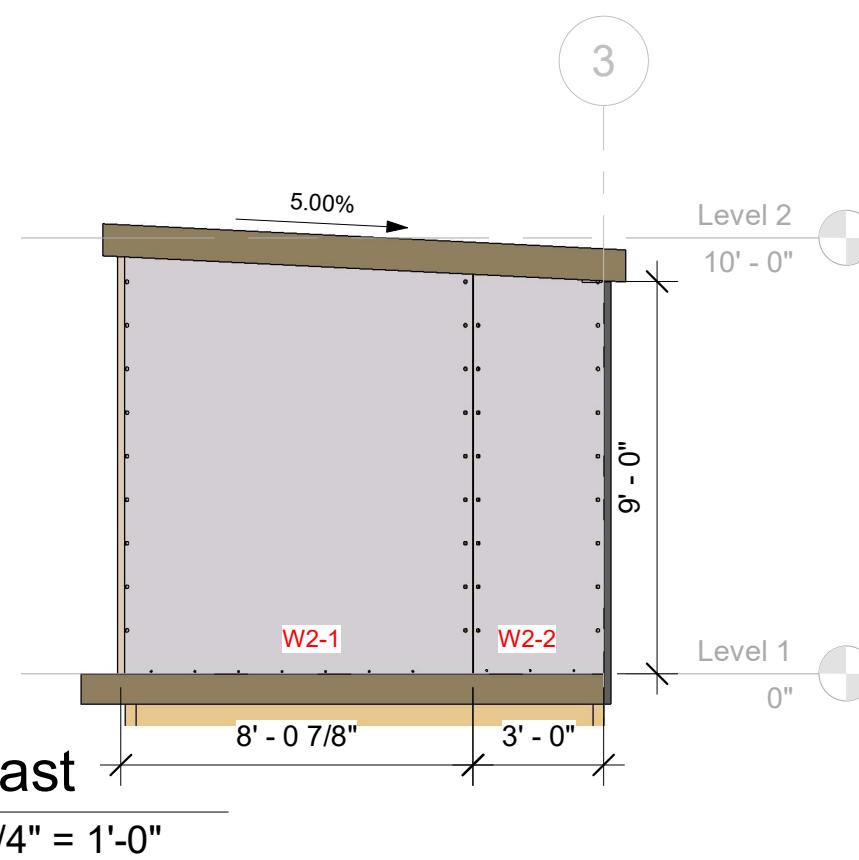

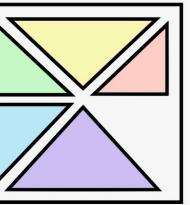

P R E F L E X  
b u i l d i n g

## MINI CABIN



P R E F L E X O F F I C E

No.	Description	Date

## Section

Project number 001

Date Issue Date

Drawn by Author

Checked by Checker


A103




Scale As indicated

08/06/2021 08:26:52 a.m.

2 Windows Detail  
 $1\frac{1}{2}'' = 1'-0''$

1 Section by Facade  
 $\frac{3}{4}'' = 1'-0''$

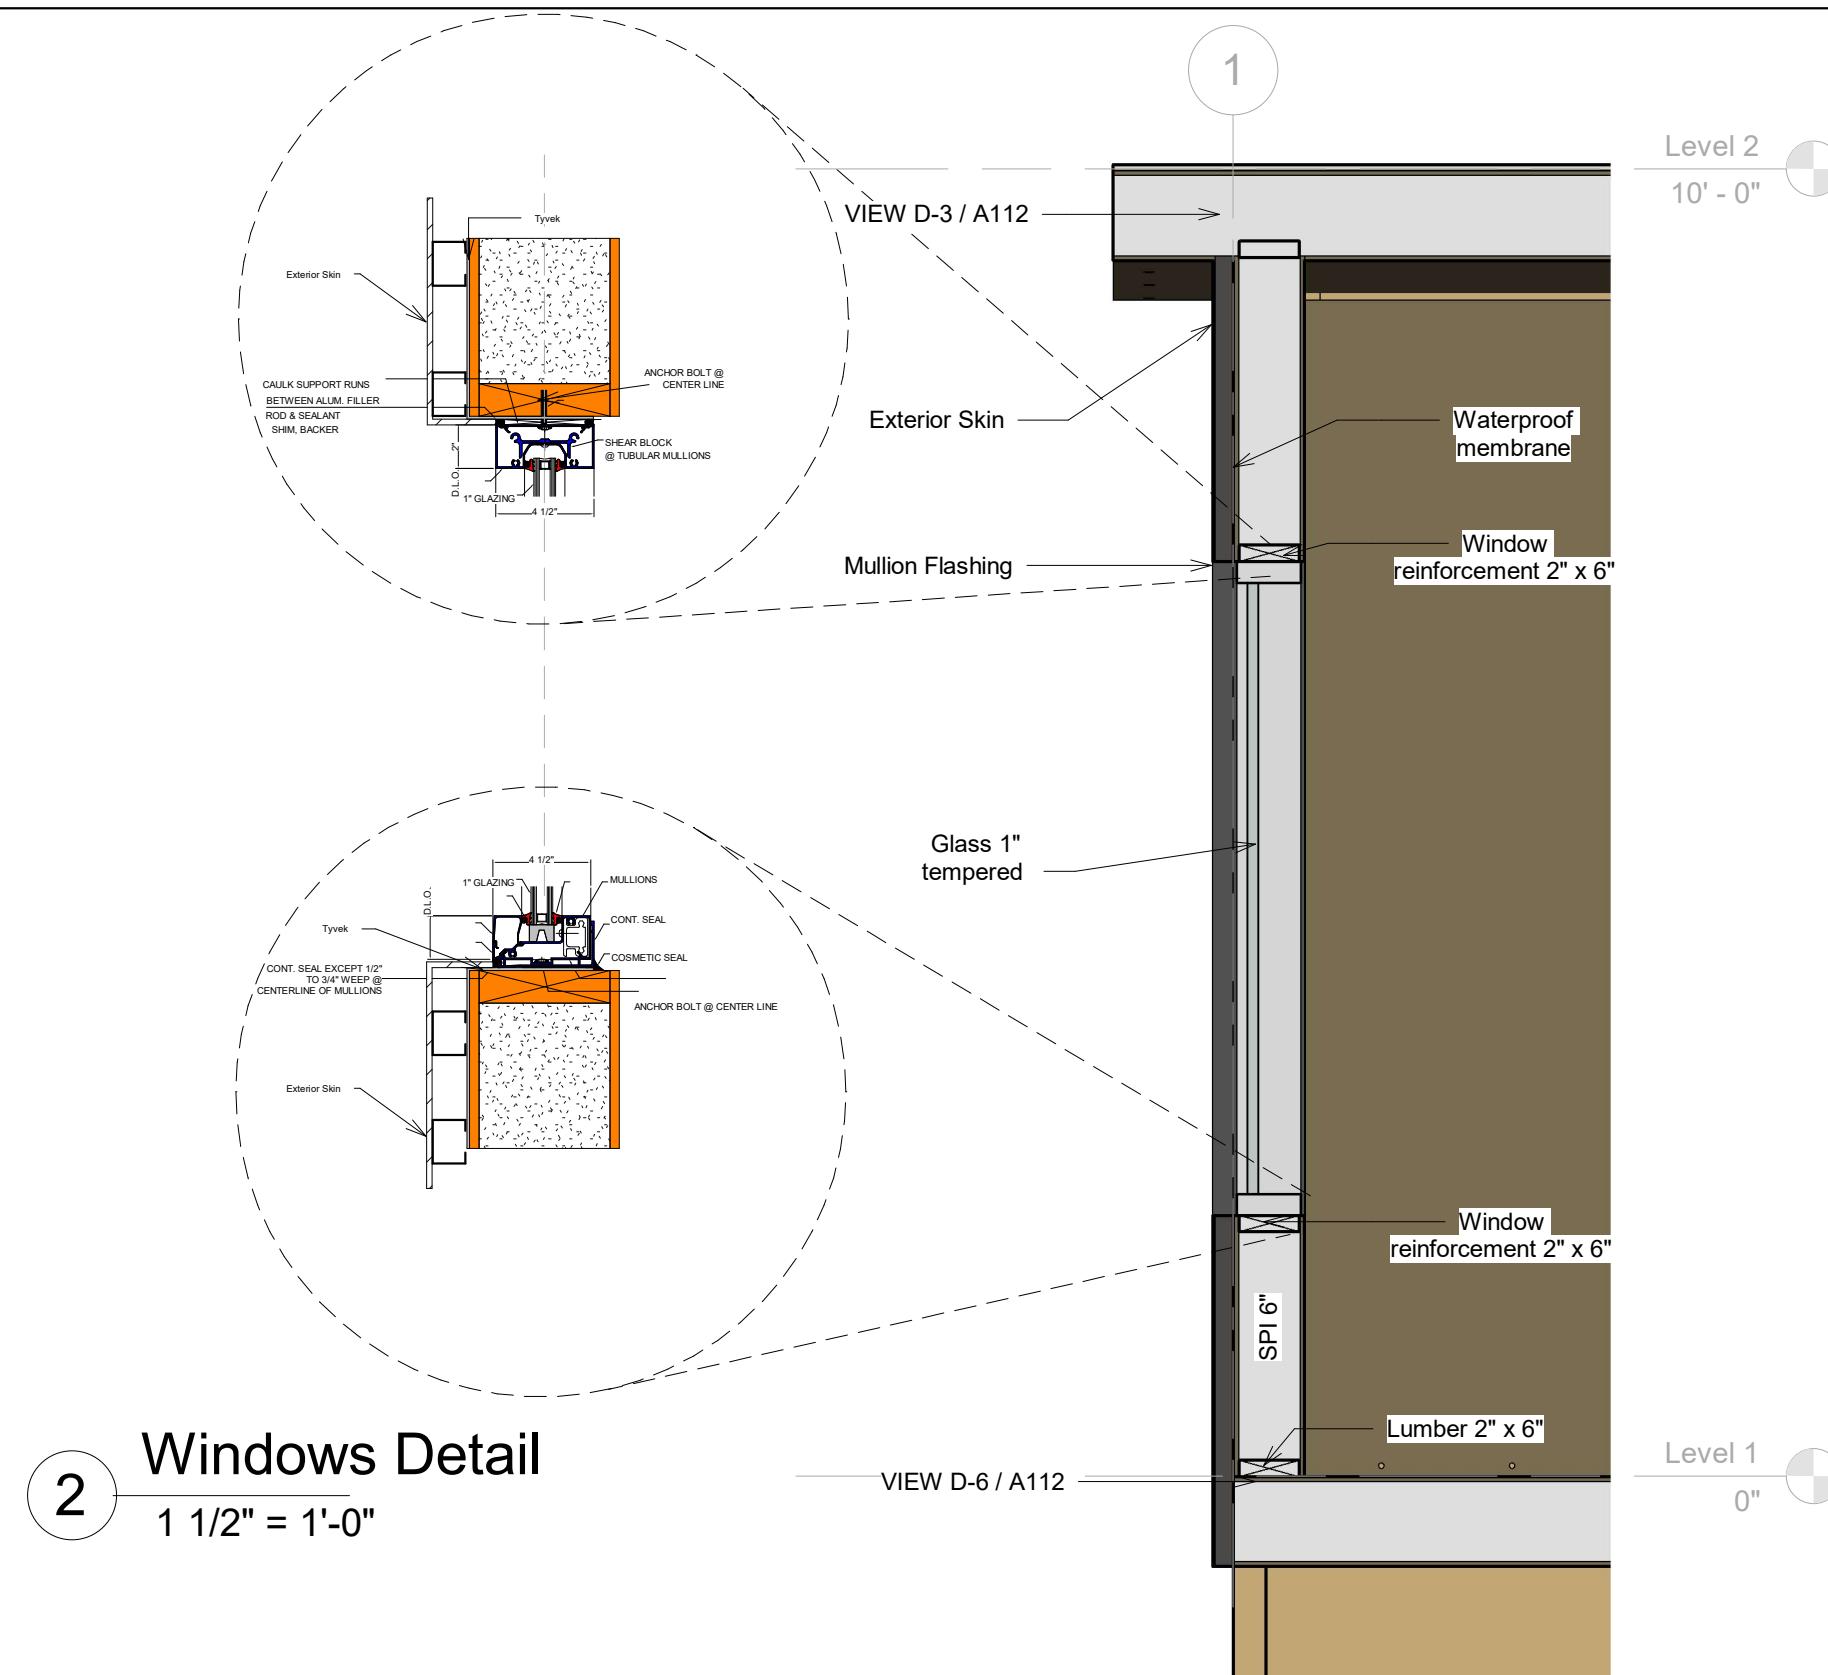

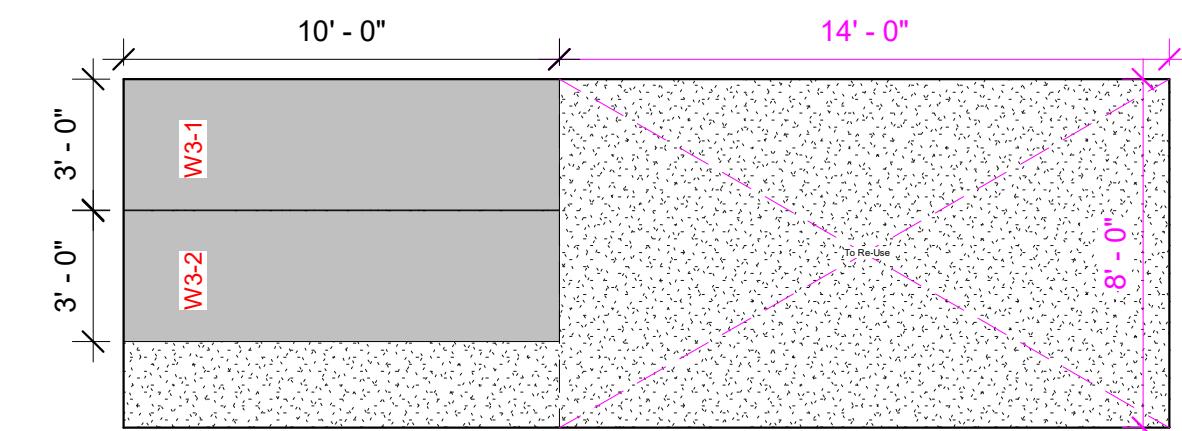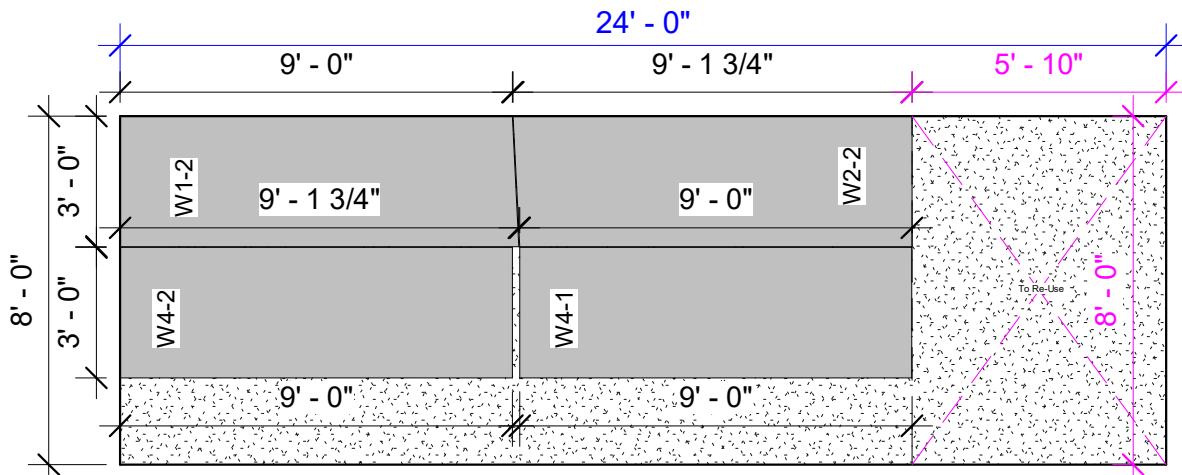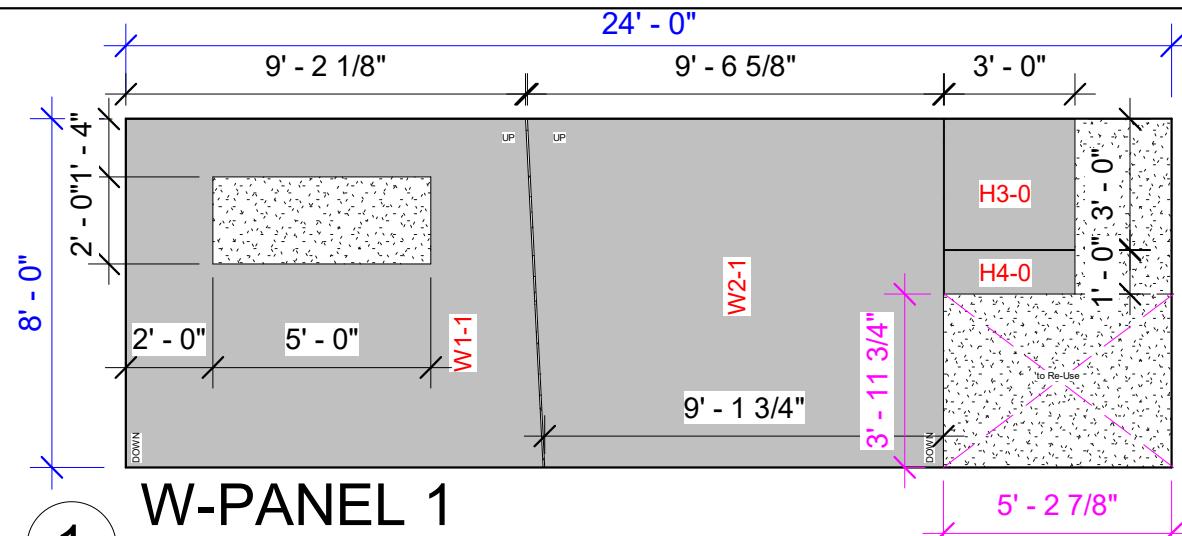

Wall Schedule			
Comments	Area	Type	Width
H4-0	2.99 SF	WALL_SPI_6"	6 5/8"
H3-0	4.74 SF	WALL_SPI_6"	6 5/8"
W4-2	26.95 SF	WALL_SPI_6"	6 5/8"
W4-1	27.00 SF	WALL_SPI_6"	6 5/8"
W1-2	27.16 SF	WALL_SPI_6"	6 5/8"
W2-2	27.16 SF	WALL_SPI_6"	6 5/8"
W3-2	28.66 SF	WALL_SPI_6"	6 5/8"
W3-1	28.71 SF	WALL_SPI_6"	6 5/8"
W1-1	64.84 SF	WALL_SPI_6"	6 5/8"
W2-1	74.84 SF	WALL_SPI_6"	6 5/8"


Grand total: 10 313.05 SF

**TOTAL WEIGHT 1,061 LBS**

3 PANEL= 576 SQFT

PANEL TO RE-USE IN OTHER PROJECT: 179.56 SF

SCRAP 13.24%

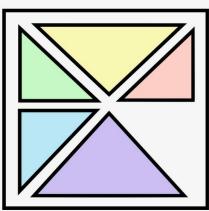

P R E F L E X  
b u i l d i n g

**MINI CABIN**




P R E F L E X O F F I C E

No.	Description	Date

**Walls\_Modulation  
for Cutting**

Project number	001
Date	Issue Date
Drawn by	Author
Checked by	Checker
A104	
Scale	1/4" = 1'-0"

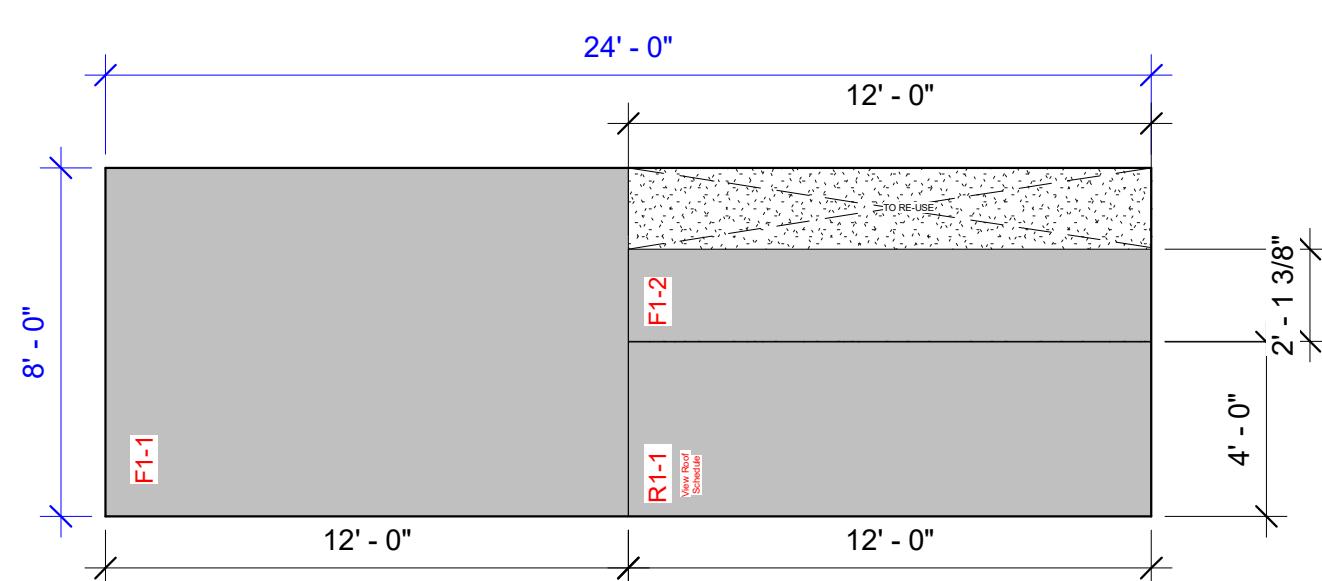


Floor Schedule			
Comments	Area	Type	Default Thickness
F1-2	96.00 SF	Floor_SPI_8"	8 1/4"
F1-2	25.38 SF	Floor_SPI_8"	8 1/4"
Grand total: 2 121.38 SF			

**TOTAL WEIGHT 432.11 LBS**

1 PANEL= 192 SQFT

PANEL TO RE-USE IN OTHER PROJECT: 24.02 SF

SCRAP 4.45%

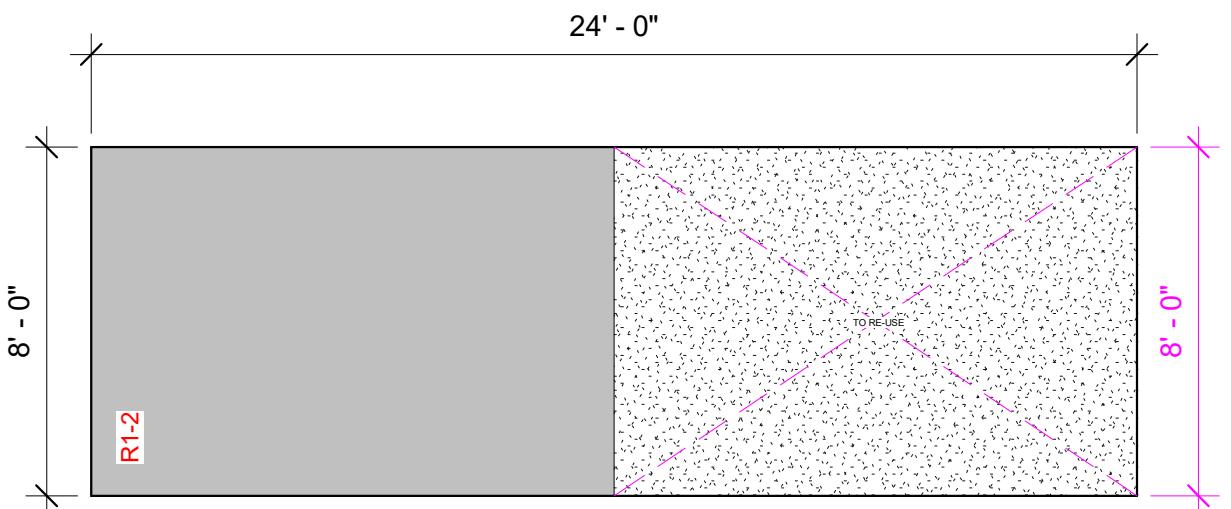

**R-PANEL 1**  
1/4" = 1'-0"


Roof Schedule			
Comments	Area	Type	Thickness
R1-1	48.01 SF	Roof_SPI_8"	8 7/8"
R1-2	96.05 SF	Roof_SPI_8"	8 7/8"
Grand total: 2 144.06 SF			

**TOTAL WEIGHT 512.85 LBS**

1 PANEL= 192 SQFT

PANEL TO RE-USE IN OTHER PROJECT: 96 SF

SCRAP 3%

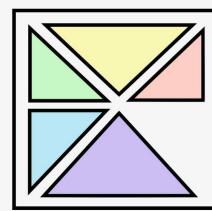

P R E F L E X  
b u i l d i n g

## MINI CABIN



P R E F L E X O F F I C E

No.	Description	Date

## Floor and Roof\_Modulation for Cutting

Project number 001


Date Issue Date

Drawn by Author

Checked by Checker

A105

Scale 1/4" = 1'-0"

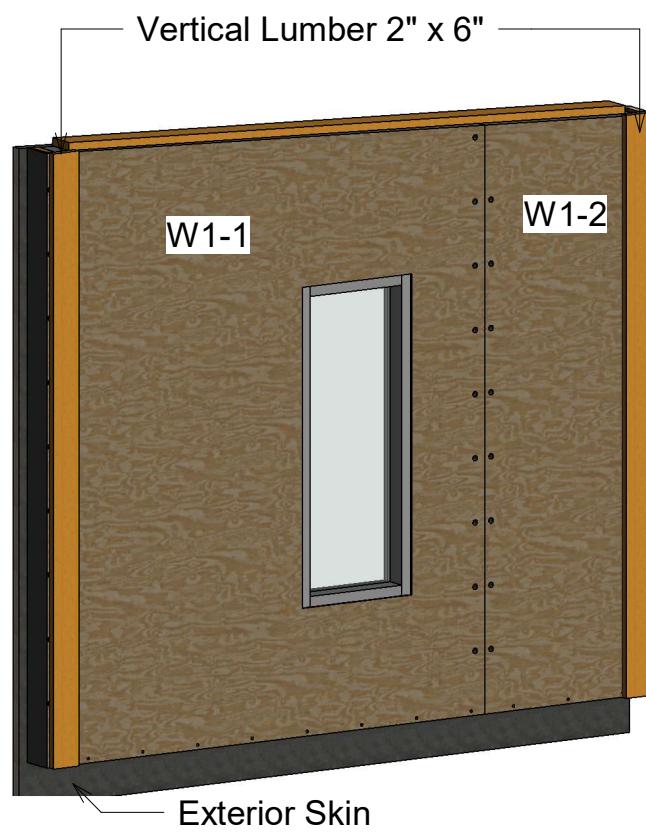

AREA: 93.81 SF  
WEIGHT: 312.38 LBS

## 1 MW\_1

### INCLUDES:

- Interior Finish
- W1-1
- Block Spline
- 2"x6" framing around window
- Window
- W1-2
- Exterior Finish




AREA: 103.72 SF  
WEIGHT: 345.38 LBS

## 2 MW\_2

### INCLUDES:

- Interior Finish
- W2-1
- Block Spline
- W2-2
- Exterior Finish

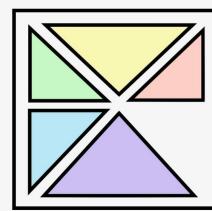

P R E F L E X  
b u i l d i n g

## MINI CABIN



P R E F L E X O F F I C E

No.	Description	Date

## Master Walls

Project number 001

Date Issue Date

Drawn by Author

Checked by Checker

A106

Scale




**MW\_3**

AREA: 77.43 SF  
WEIGHT: 257.84 LBS

**INCLUDES:**

- Interior Finish
- W3-1
- Block Spline
- Block Spline
- 2"x6" framing around door
- Door
- H3-0
- W3-2
- Exterior Finish

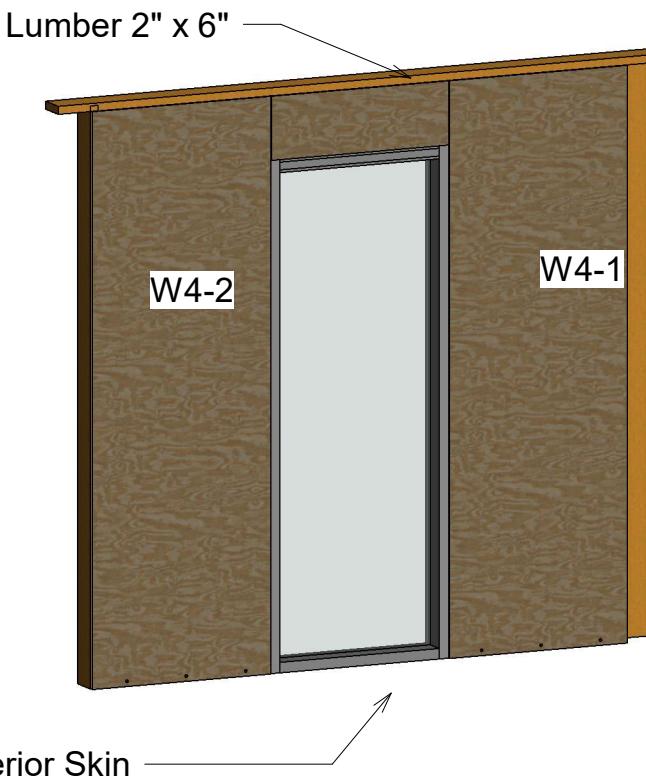


**MW\_4**

AREA: 68.42 SF  
WEIGHT: 227.83LBS

**INCLUDES:**

- Interior Finish
- W4-1
- Block Spline
- Block Spline
- Window
- H4-0
- W4-2
- Exterior Finish

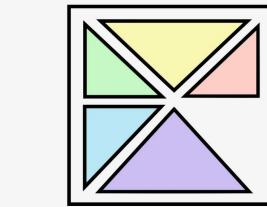

P R E F L E X  
b u i l d i n g

**MINI CABIN**



P R E F L E X O F F I C E

No.	Description	Date

**Master Walls**

Project number  
001


Date Issue Date


Drawn by Author

Checked by Checker

A107

Scale

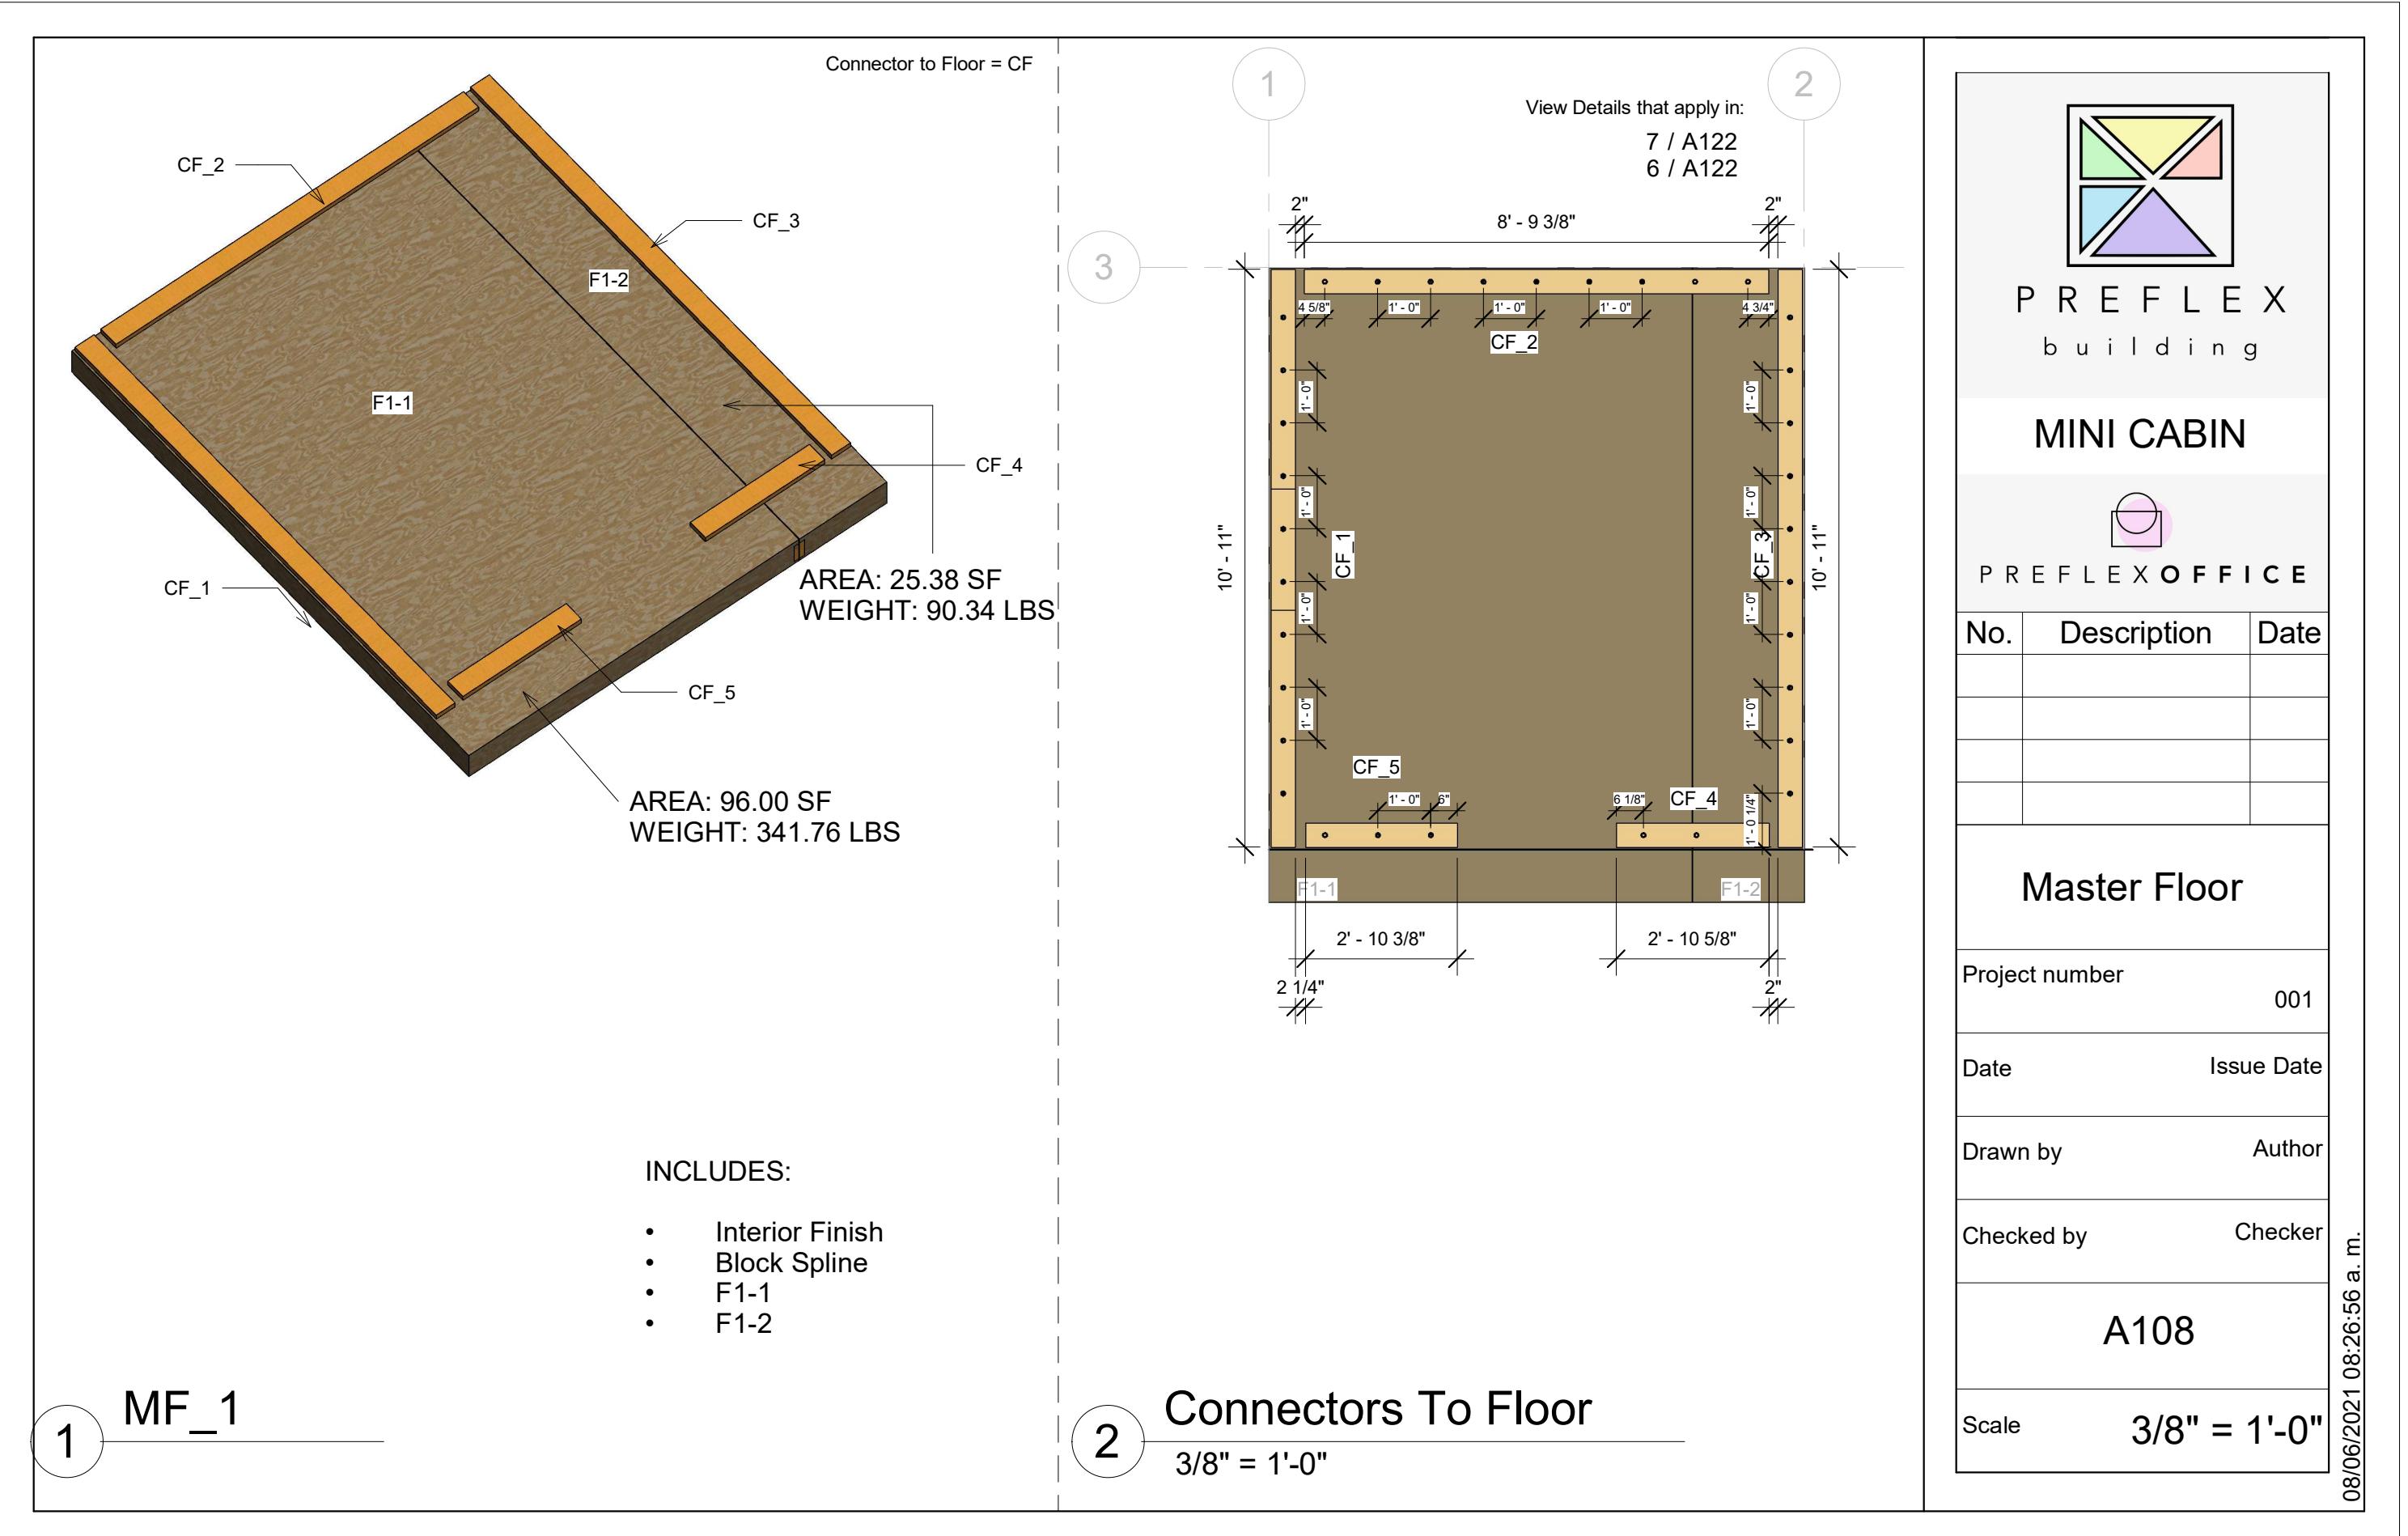


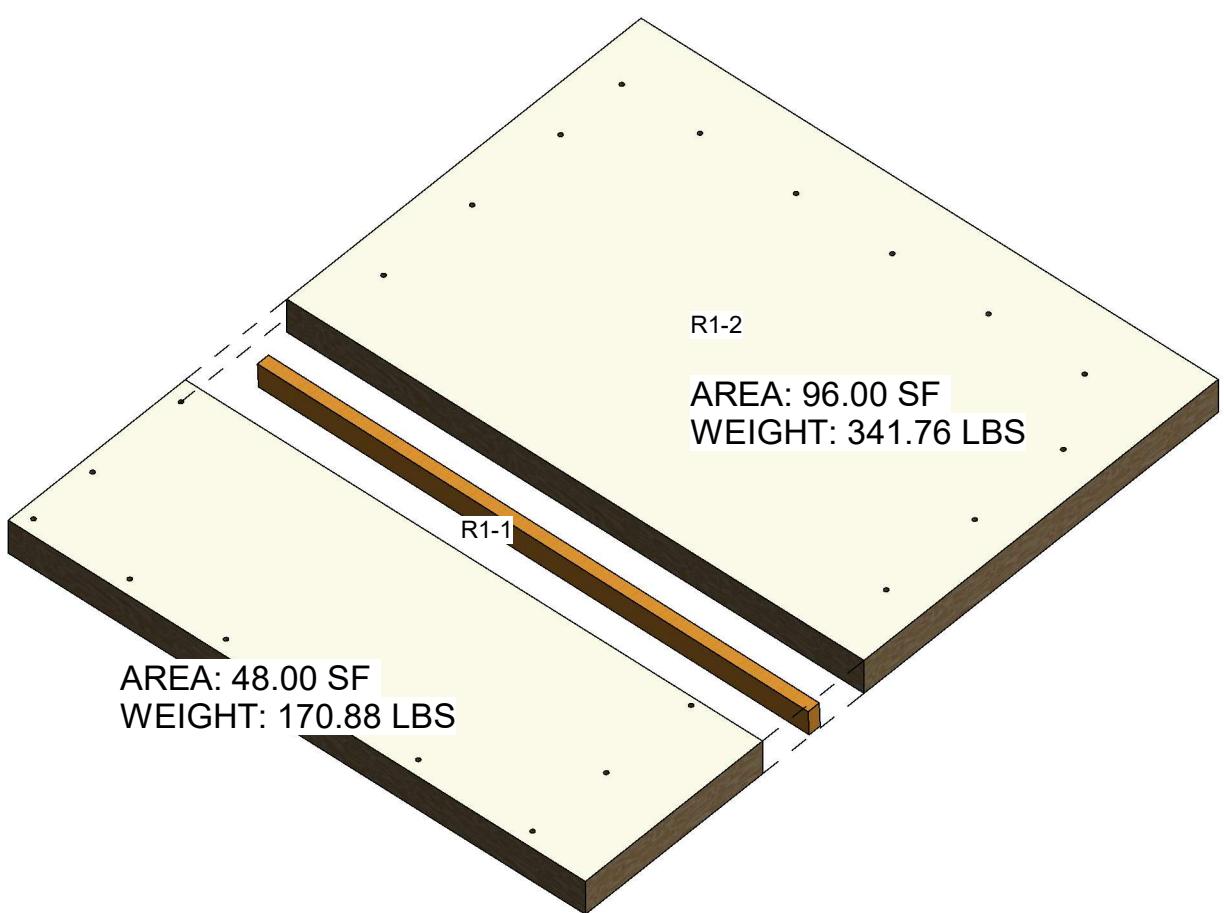

INCLUDES:

- Interior Finish
- Block Spline
- Exterior Finish

1 MR\_1

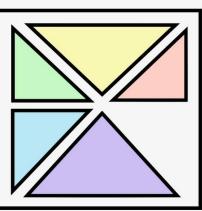

PREFLEX  
building

MINI CABIN



PREFLEX OFFICE

No.	Description	Date

Master Roof

Project number 001


Date Issue Date

Drawn by Author

Checked by Checker


A109

Scale

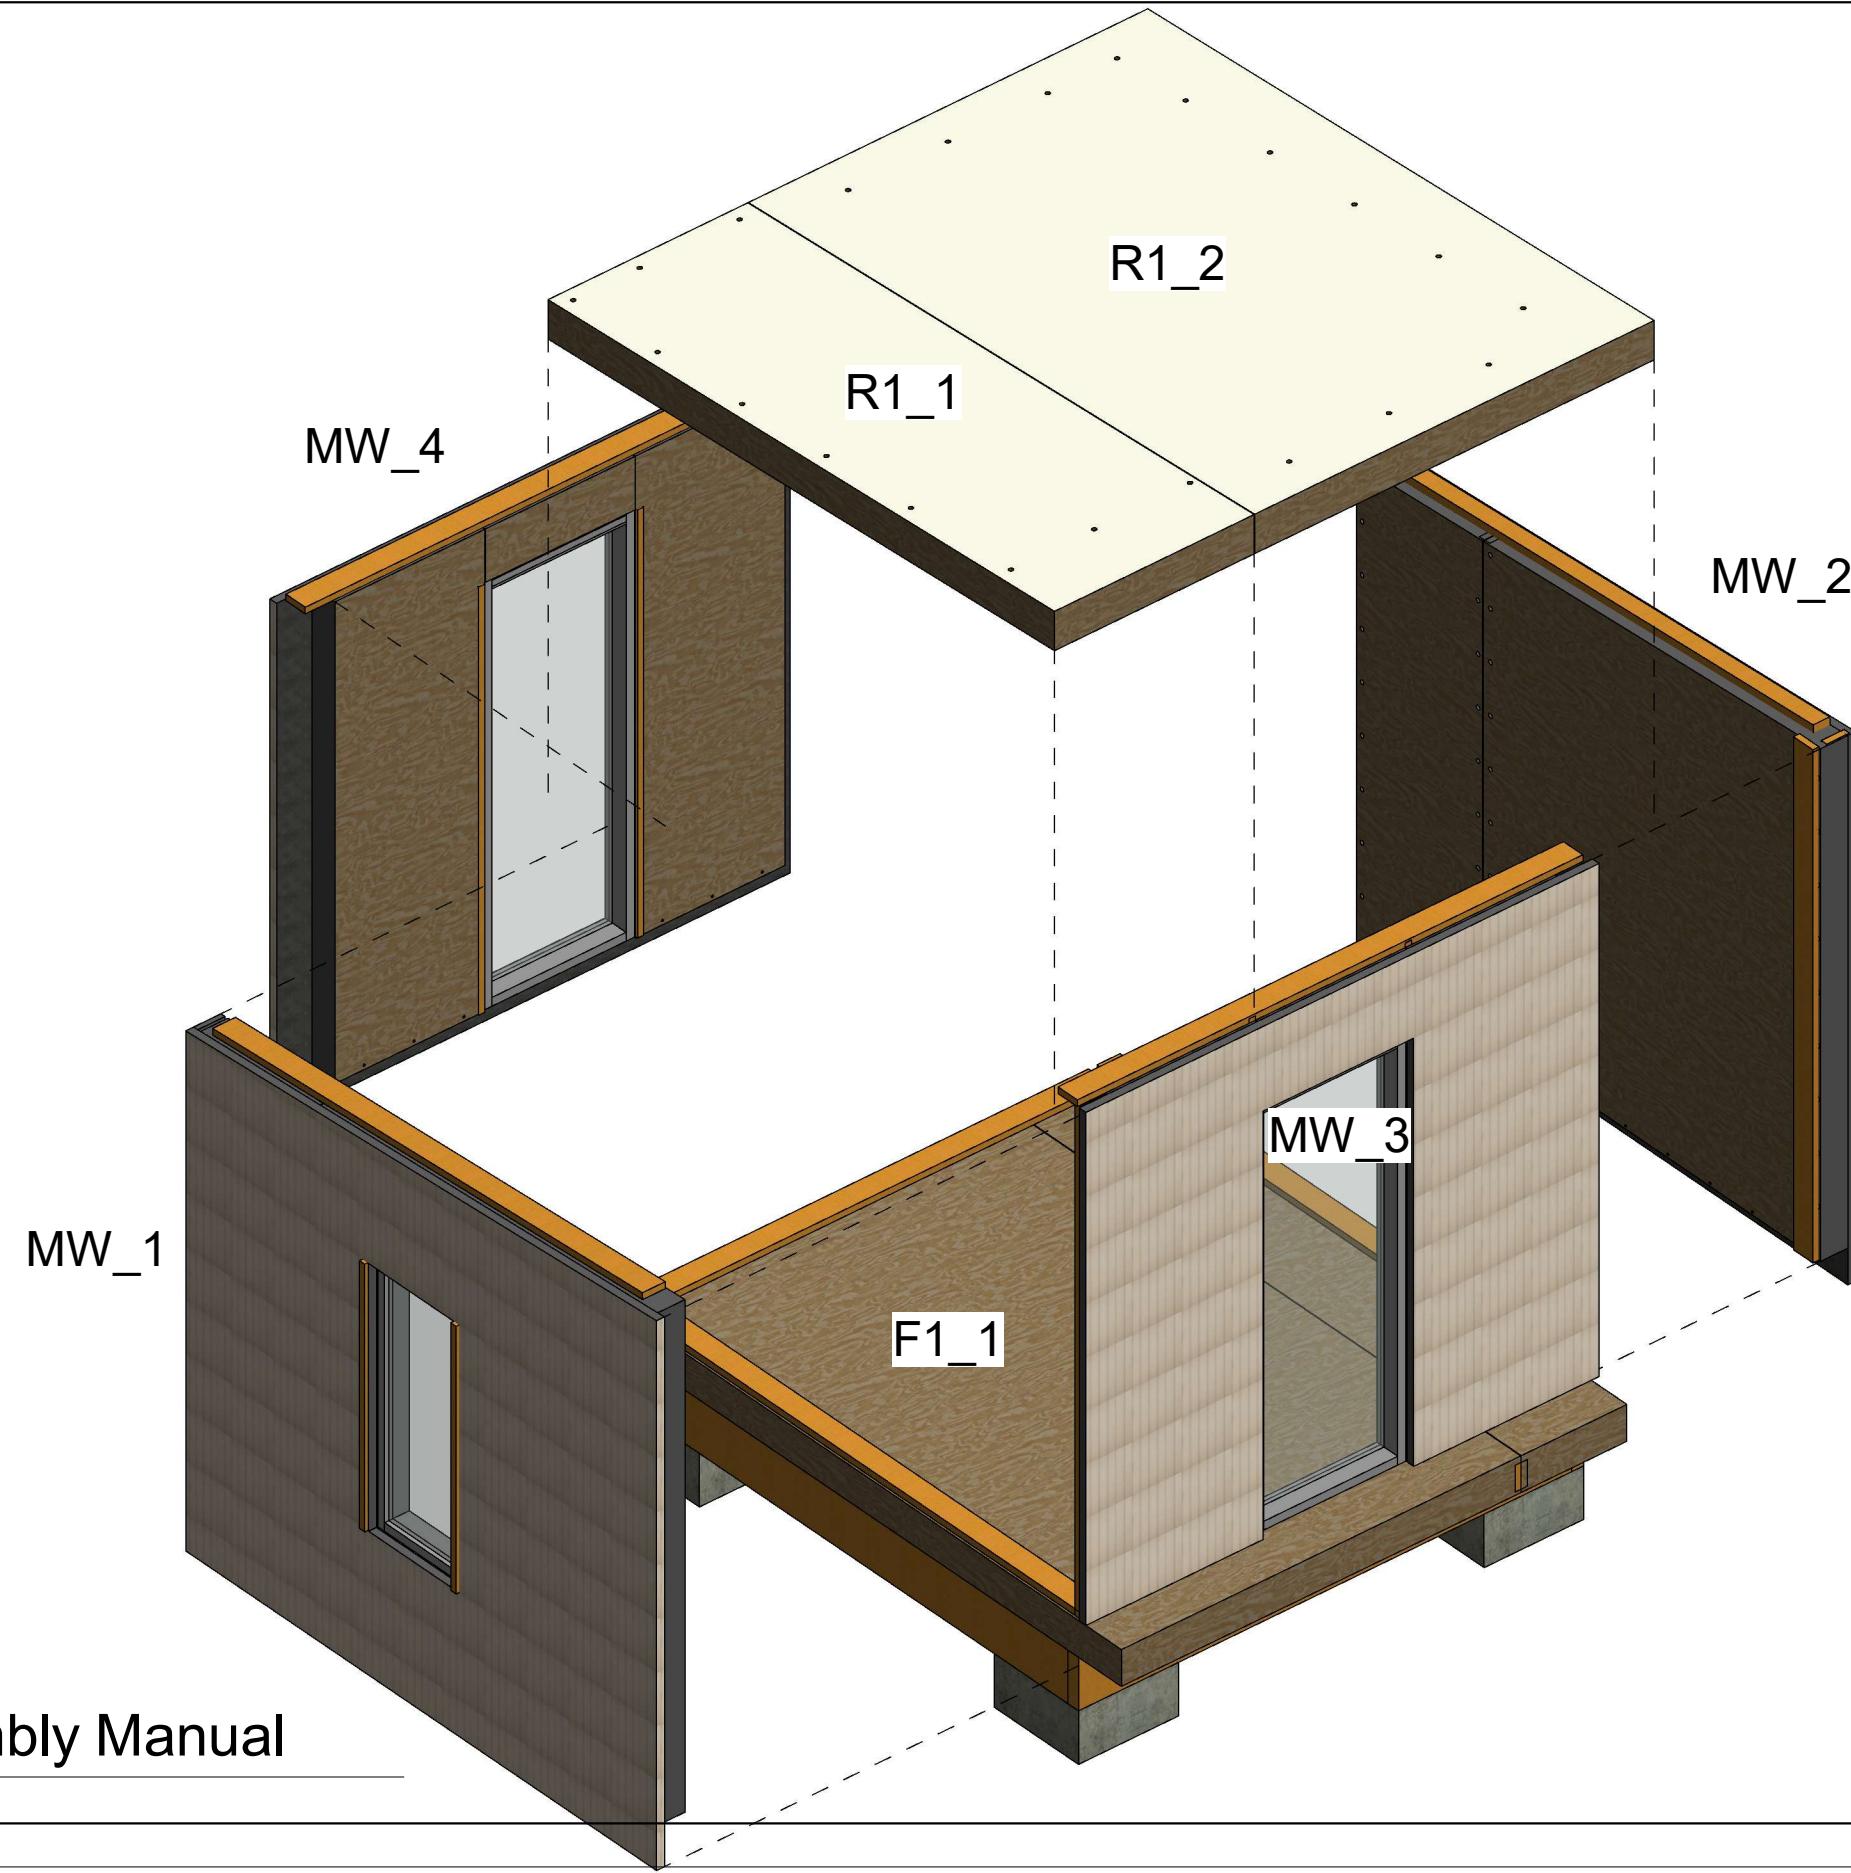

1

## Assembly Manual

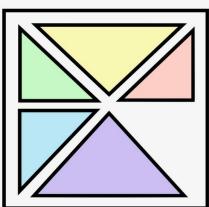

PREFLEX  
building

### MINI CABIN



PREFLEX OFFICE

No.	Description	Date

### Assembly Manual

Project number 001


Date Issue Date


Drawn by Author


Checked by Checker

A110

Scale

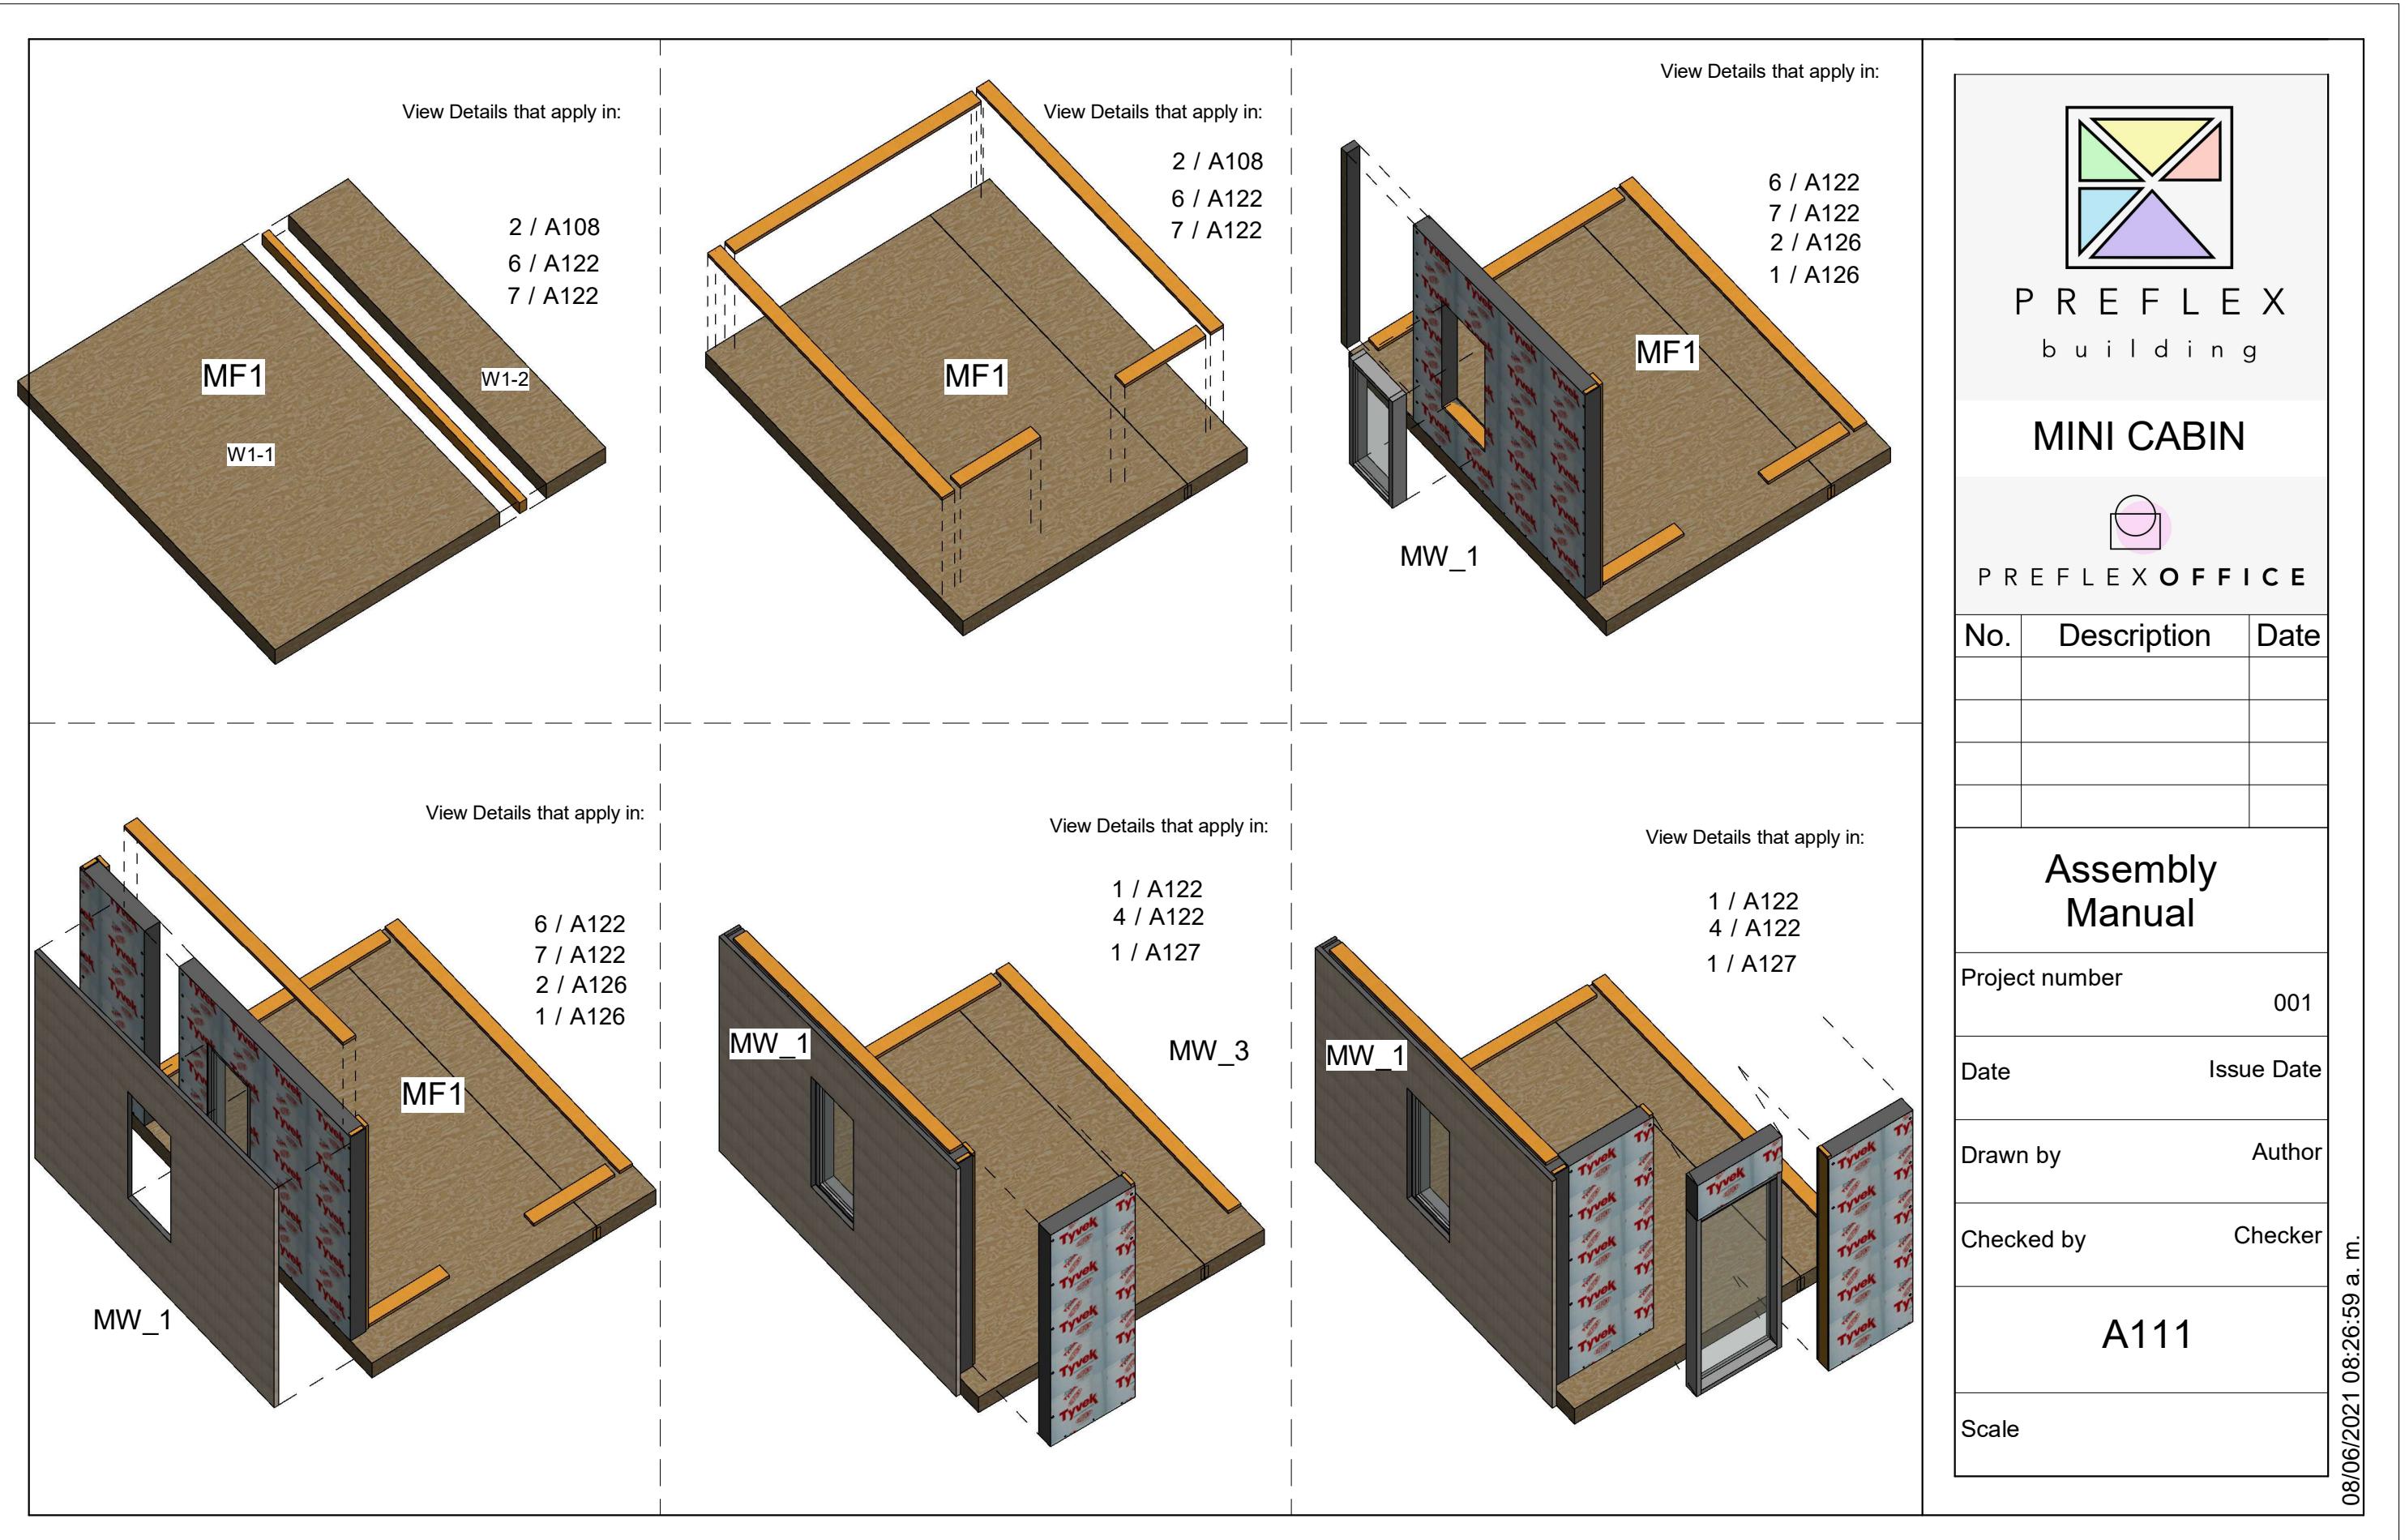

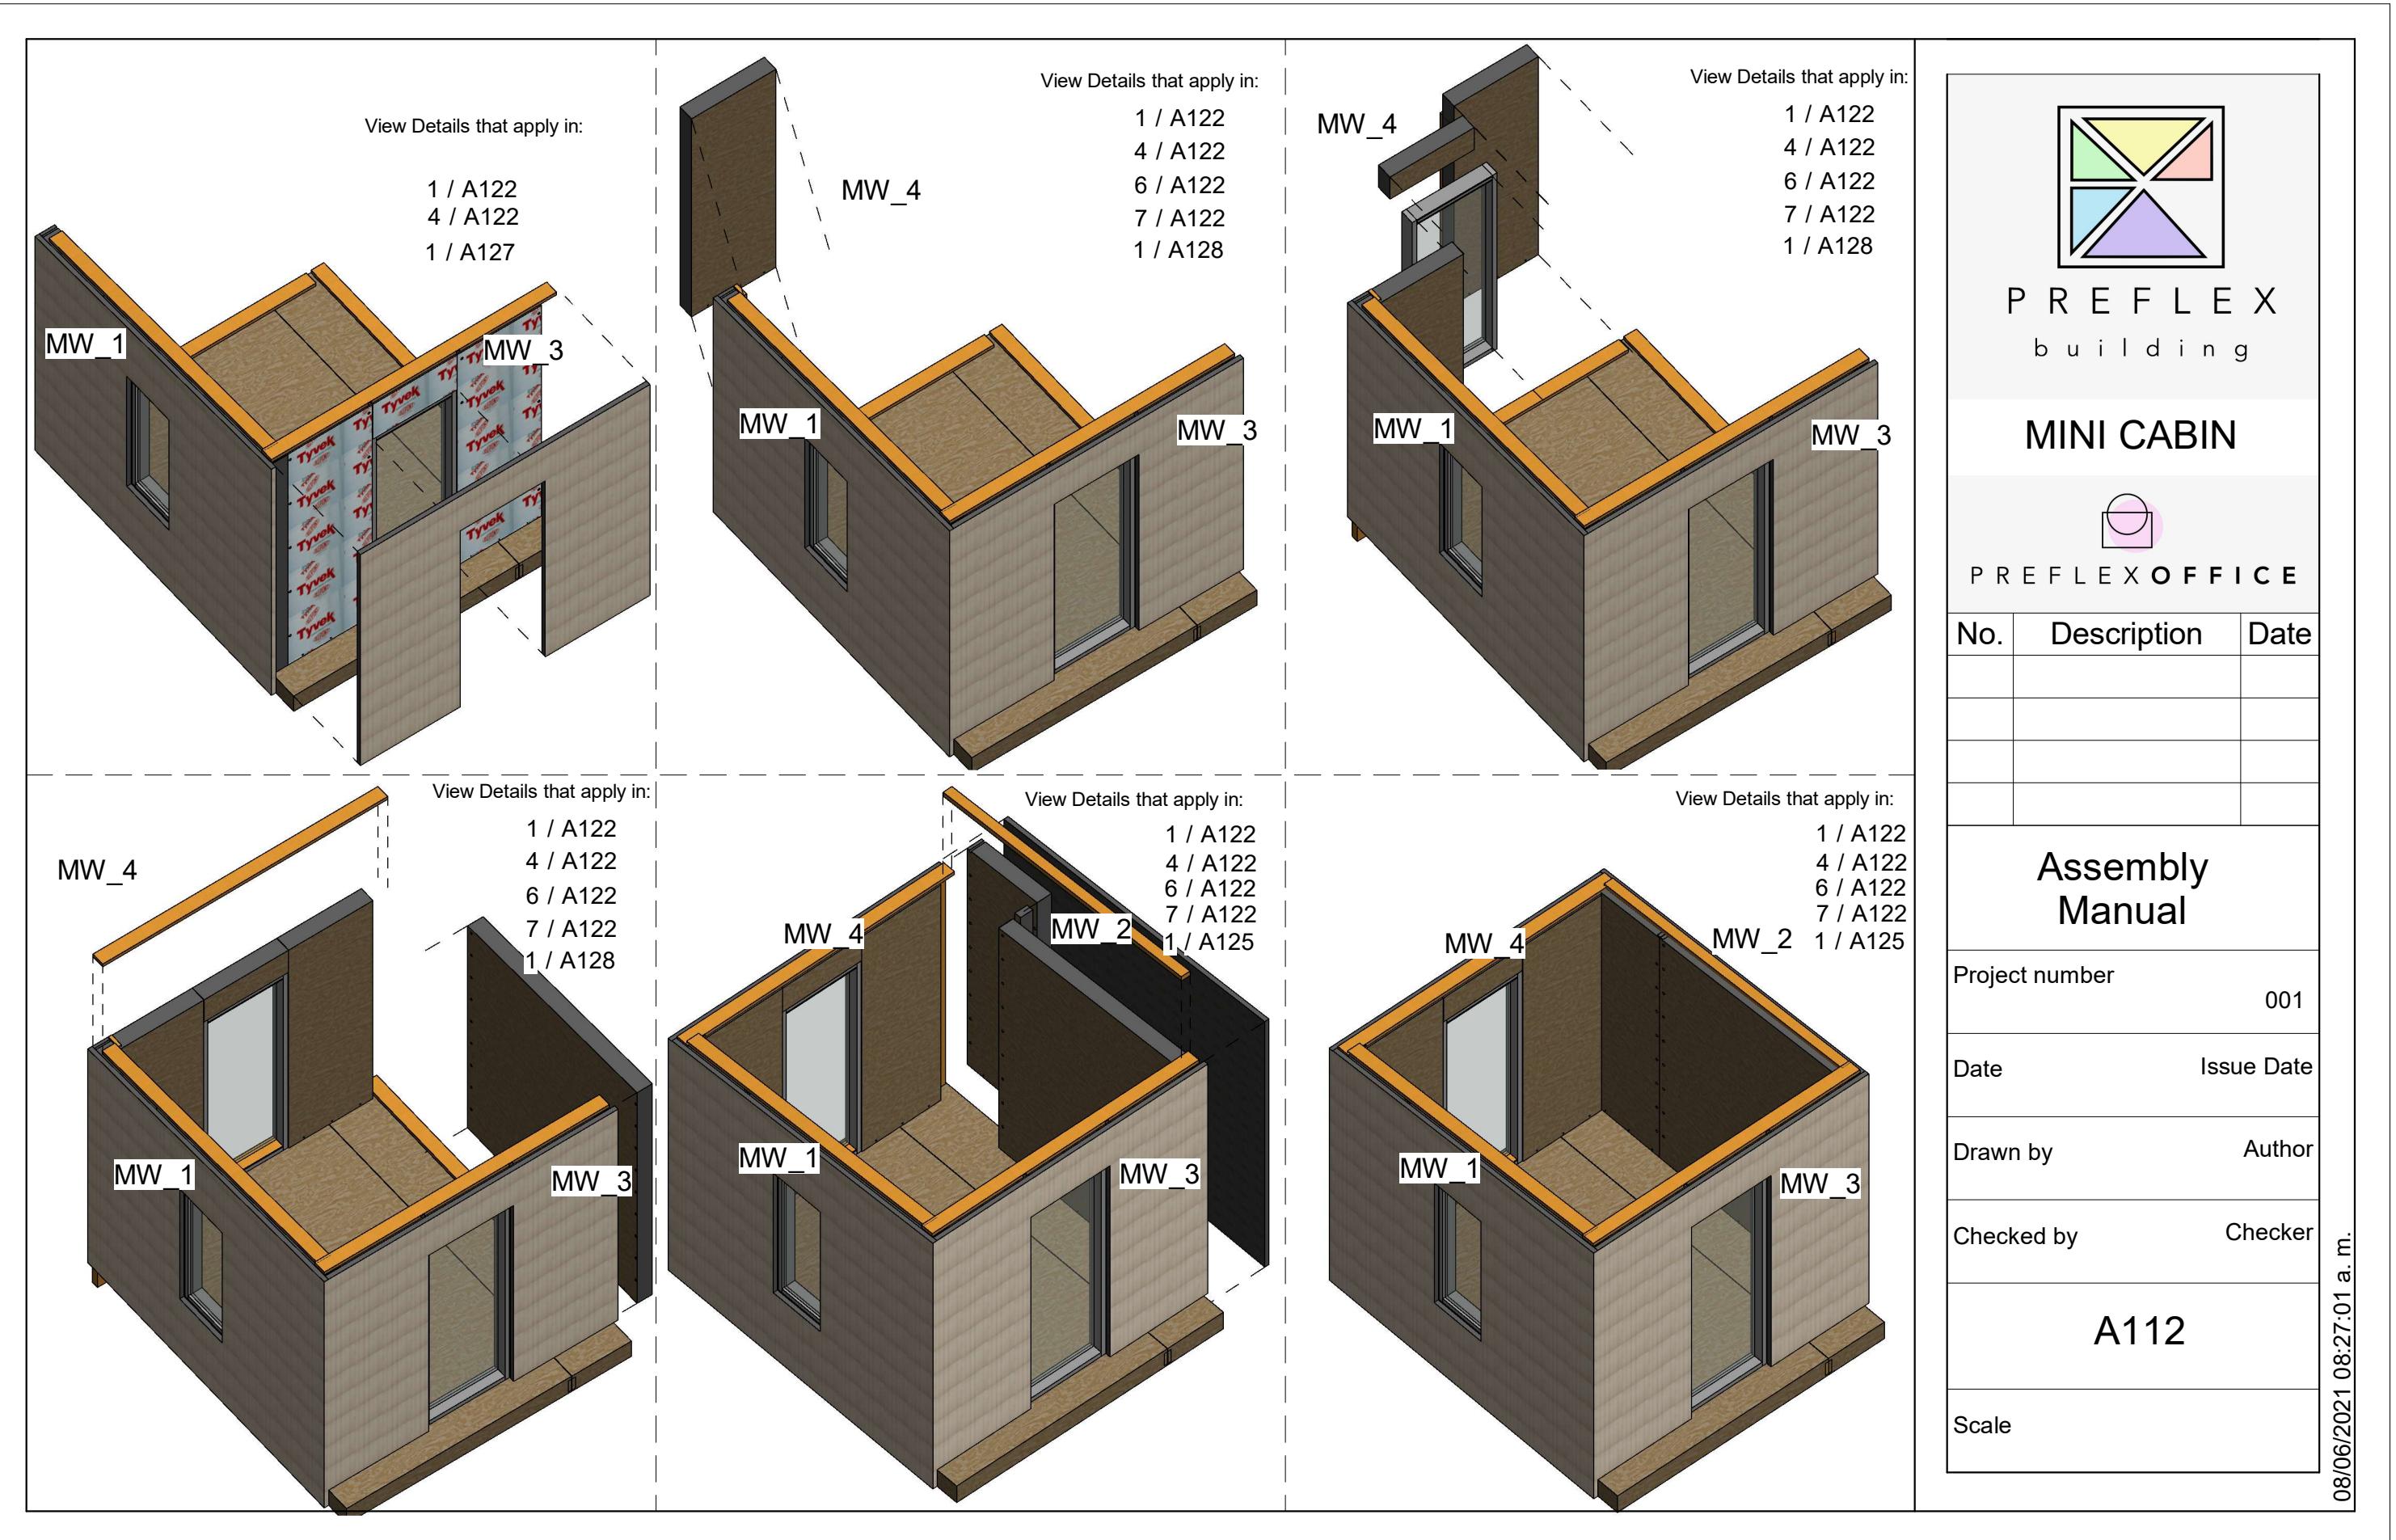

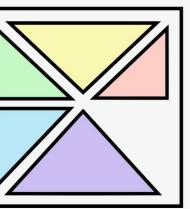

P R E F L E X  
b u i l d i n g

## MINI CABIN



P R E F L E X O F F I C E

No.	Description	Date

## Assembly Manual

Project number 001

Date Issue Date

Drawn by Author

Checked by Checker


A113

Scale

08/06/2021 08:27:02 a.m.


View Details that apply in:


2 / A122  
3 / A122  
2 / A105  
1 / A130  
2 / A130

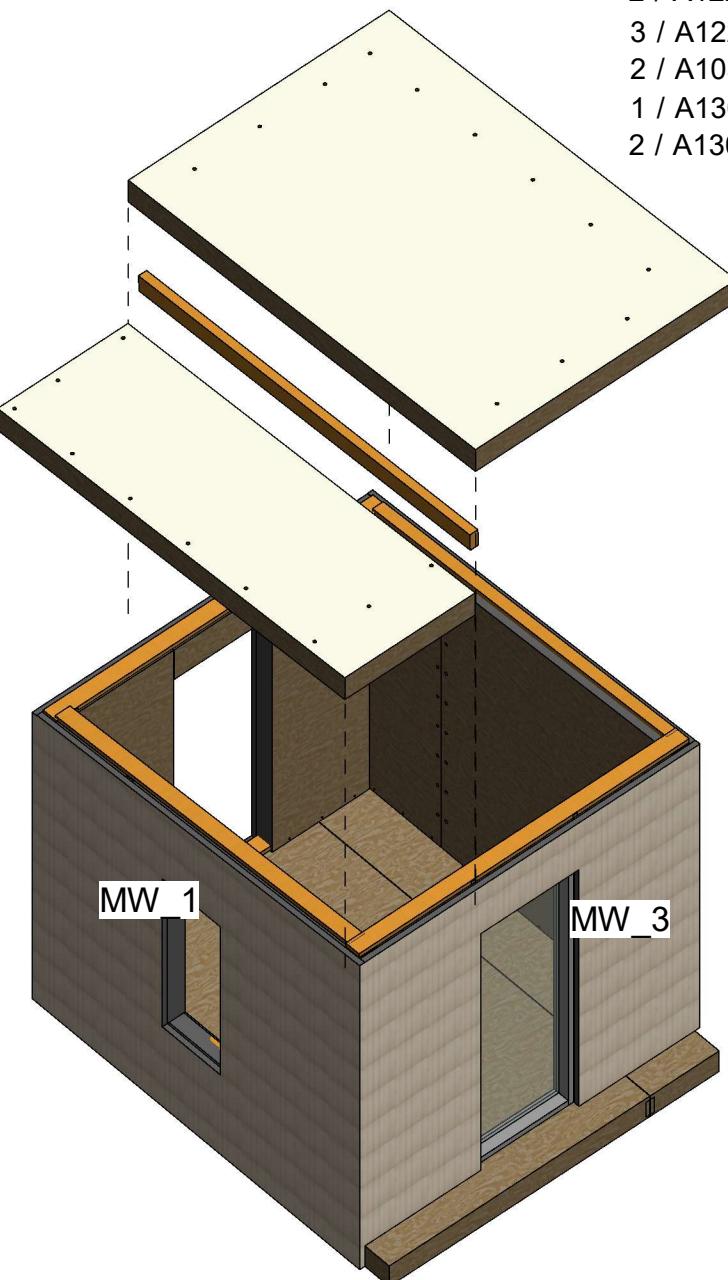

View Details that apply in:

2 / A122  
3 / A122  
2 / A105  
1 / A130  
2 / A130

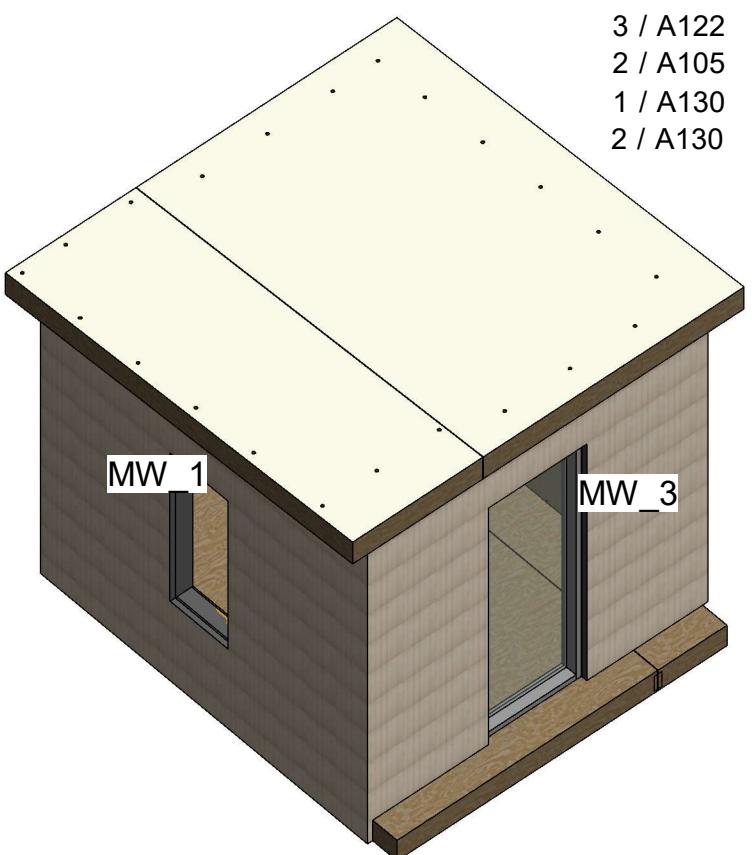

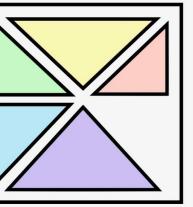

PREFLEX  
building

## MINI CABIN



### PREFLEX OFFICE

No.	Description	Date
-----	-------------	------

## Details

Project number	001
----------------	-----

Date	Issue Date
------	------------


Drawn by	Author
----------	--------

Checked by	Checker
------------	---------


A122

Scale	As indicated
-------	--------------


08/06/2021 08:27:03 a.m.

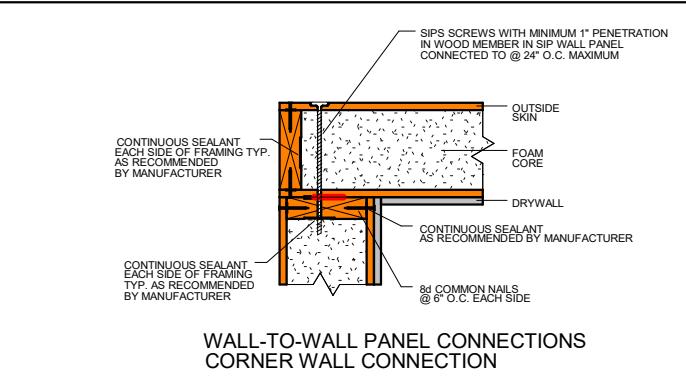


**1** Wall to wall\_Corner  
1" = 1'-0"

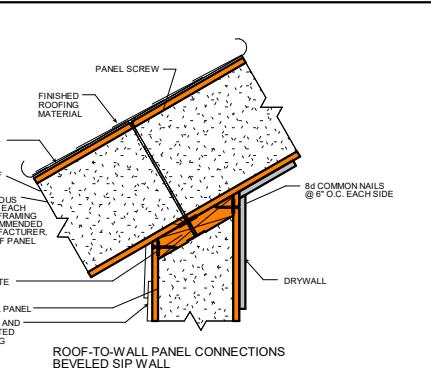


**2** Roof to Wall\_Beveled  
1" = 1'-0"

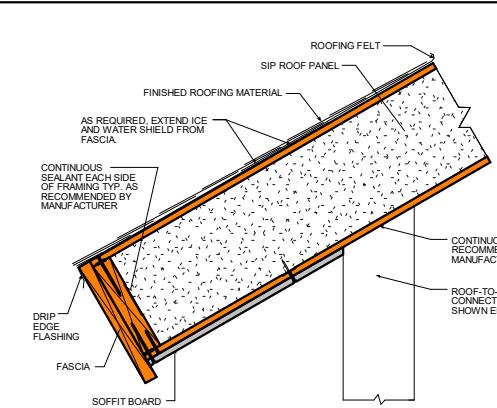



**3** Roof to Walls\_Eaves  
3/4" = 1'-0"

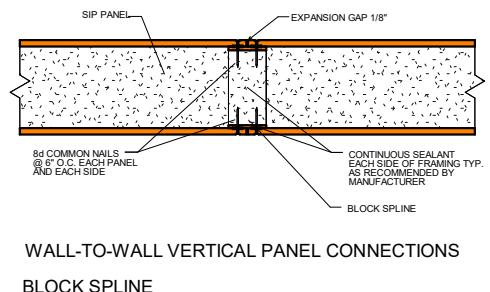

**4** Wall to wall\_Block Spline  
1" = 1'-0"

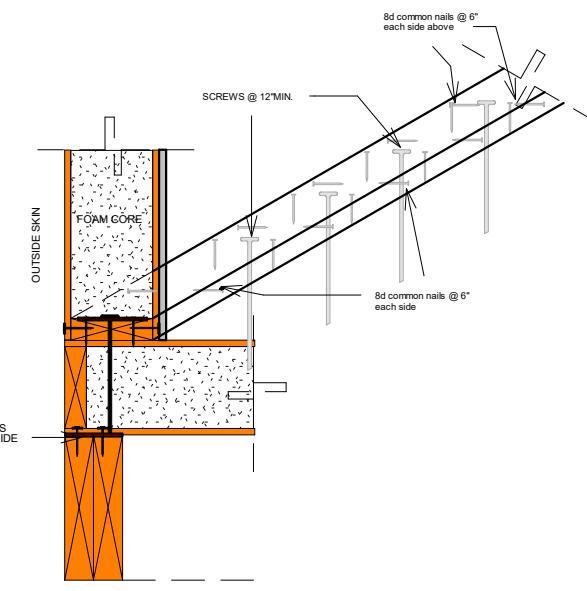



**7** Nails and Screws on floor  
1" = 1'-0"

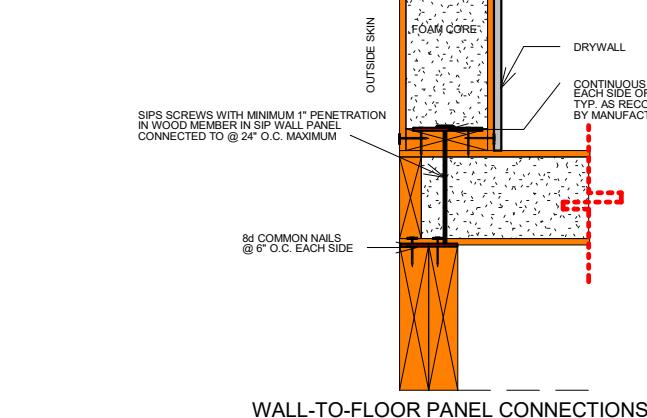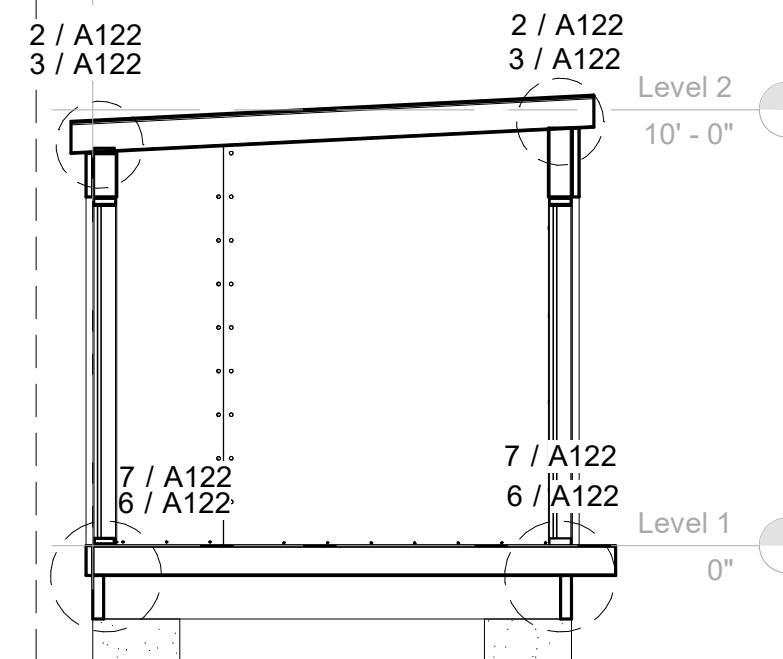

**6** Floor to Wall  
1" = 1'-0"

**5** Section 1  
1/4" = 1'-0"

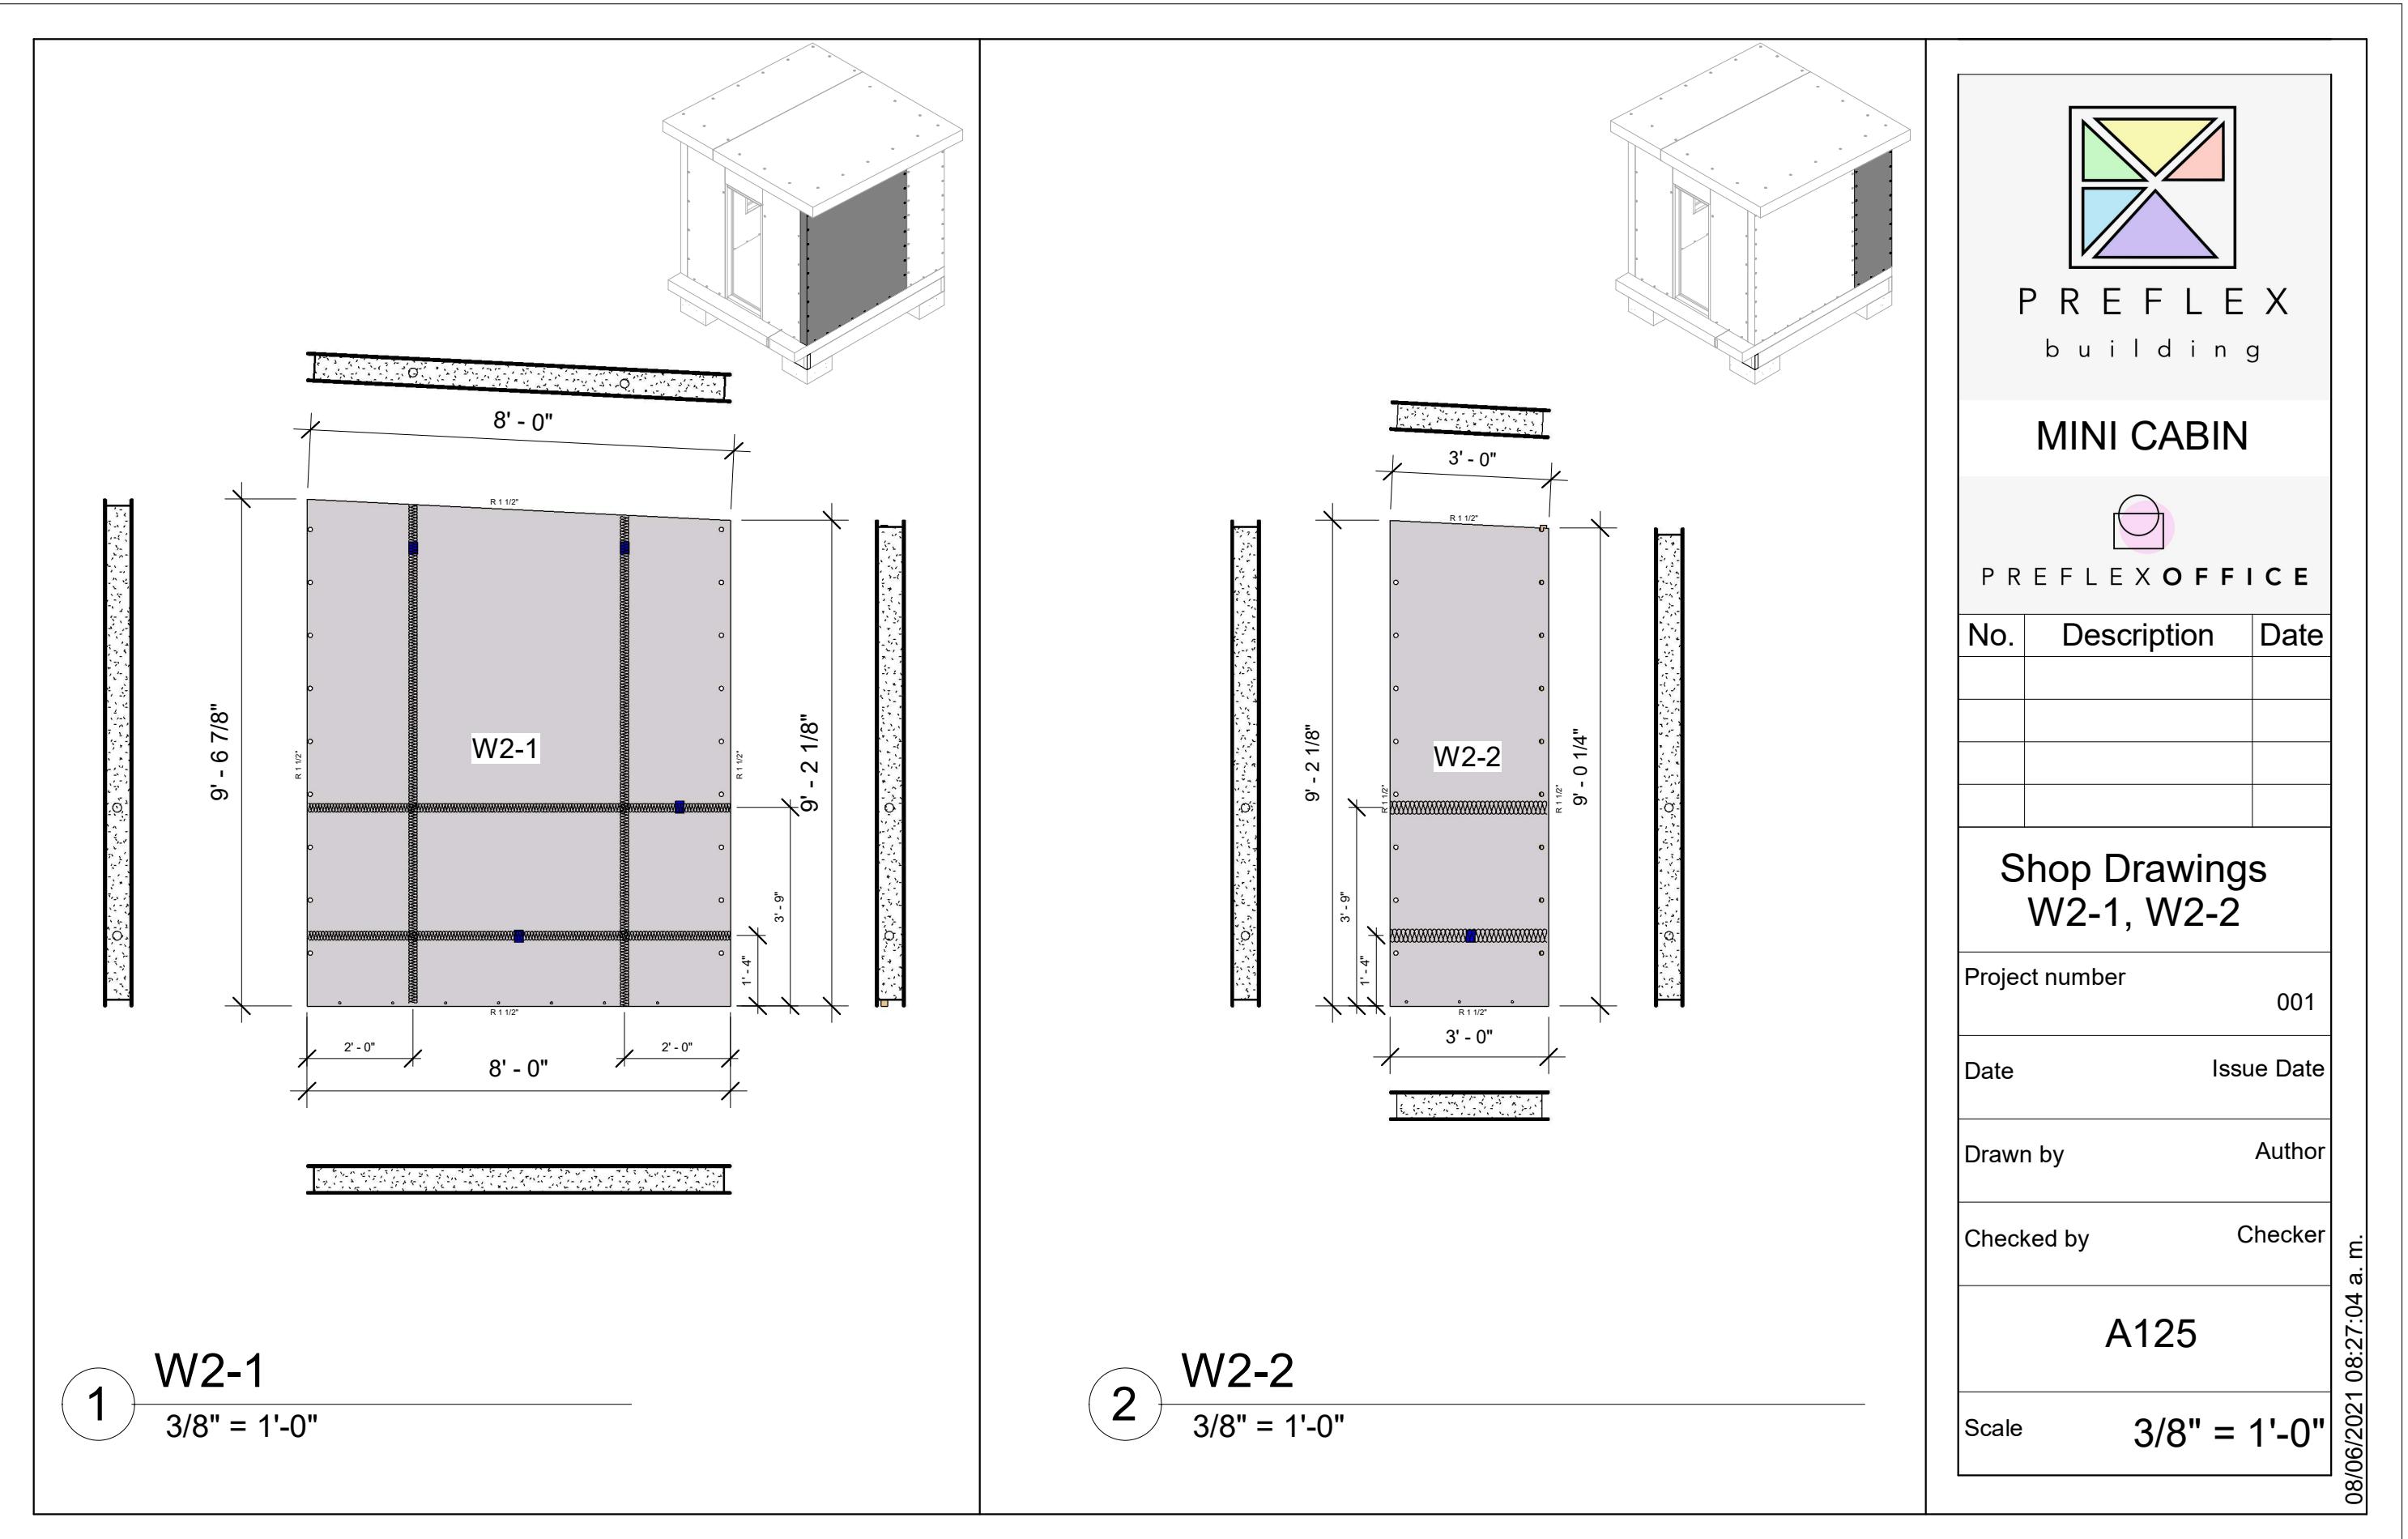

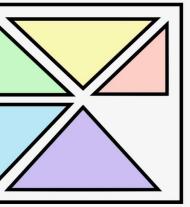

P R E F L E X  
b u i l d i n g

## MINI CABIN



### P R E F L E X O F F I C E

No.	Description	Date



## Shop Drawings W1-2, W1-1

Project number	001
Date	Issue Date
Drawn by	Author
Checked by	Checker


A126

Scale  $3/8" = 1'-0"$



08/06/2021 08:27:06 a.m.

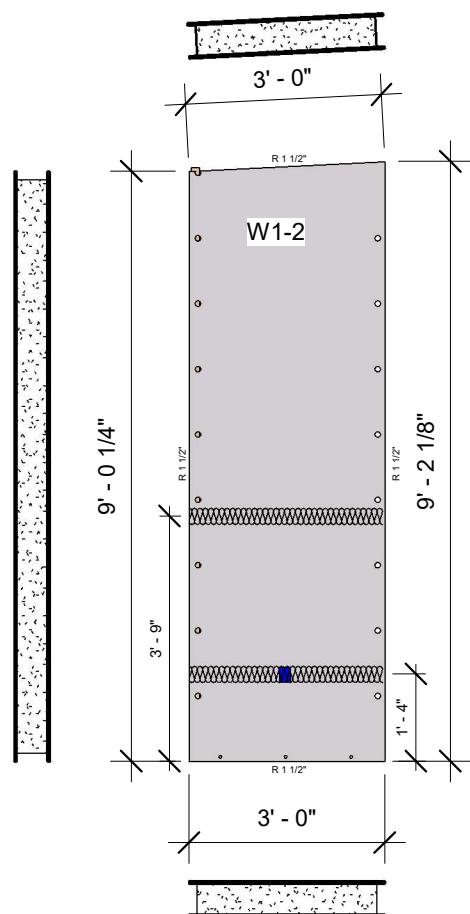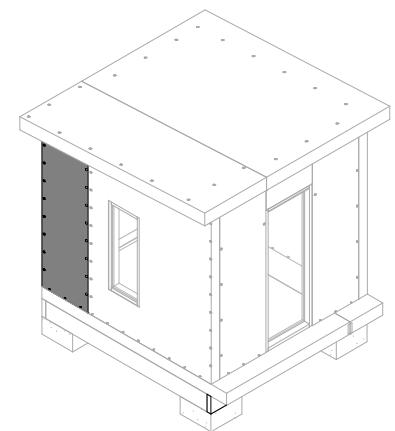

1 W1-2  
 $3/8" = 1'-0"$

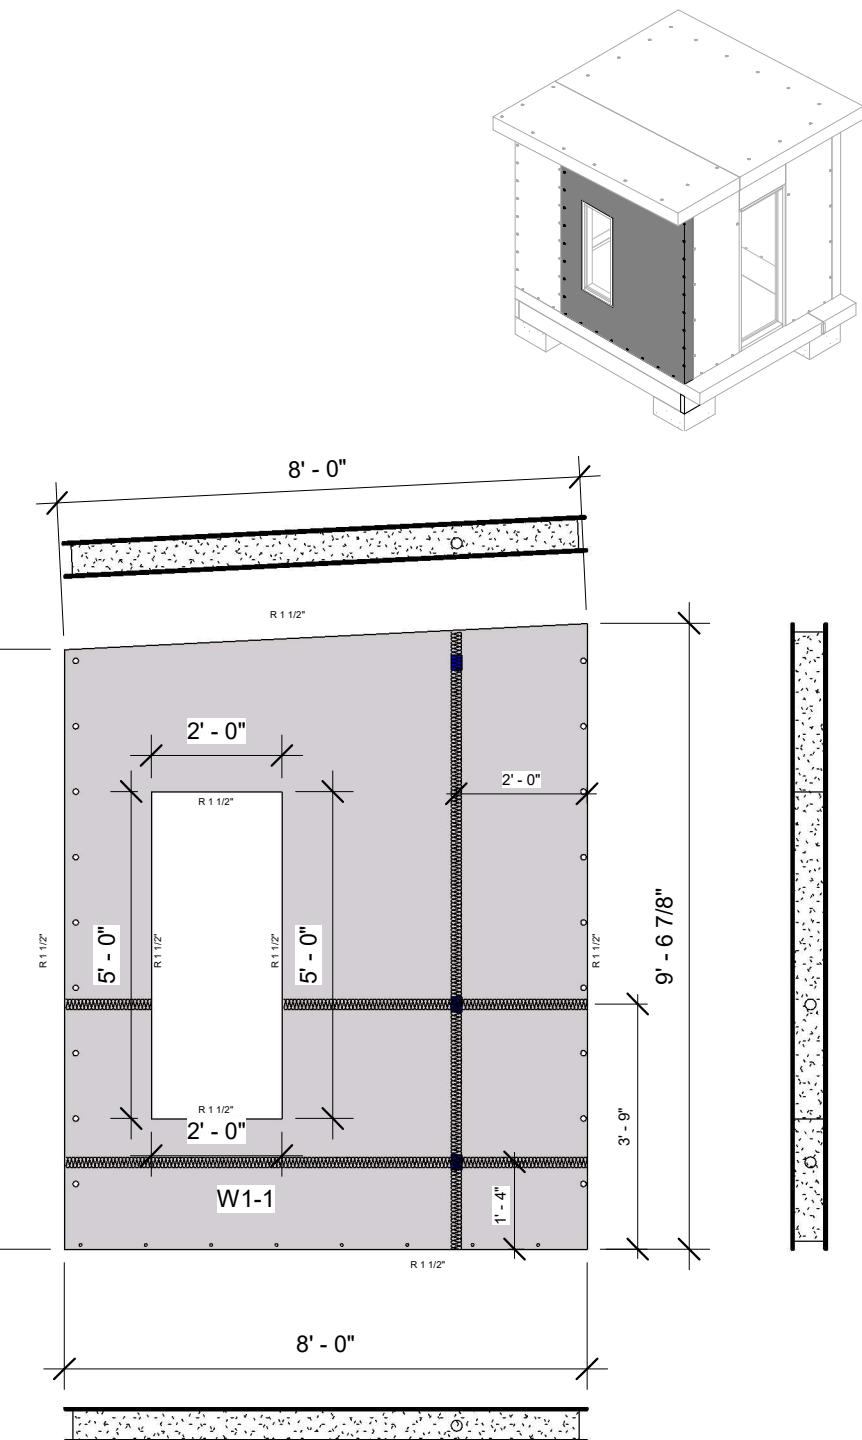

2 W1-1  
 $3/8" = 1'-0"$

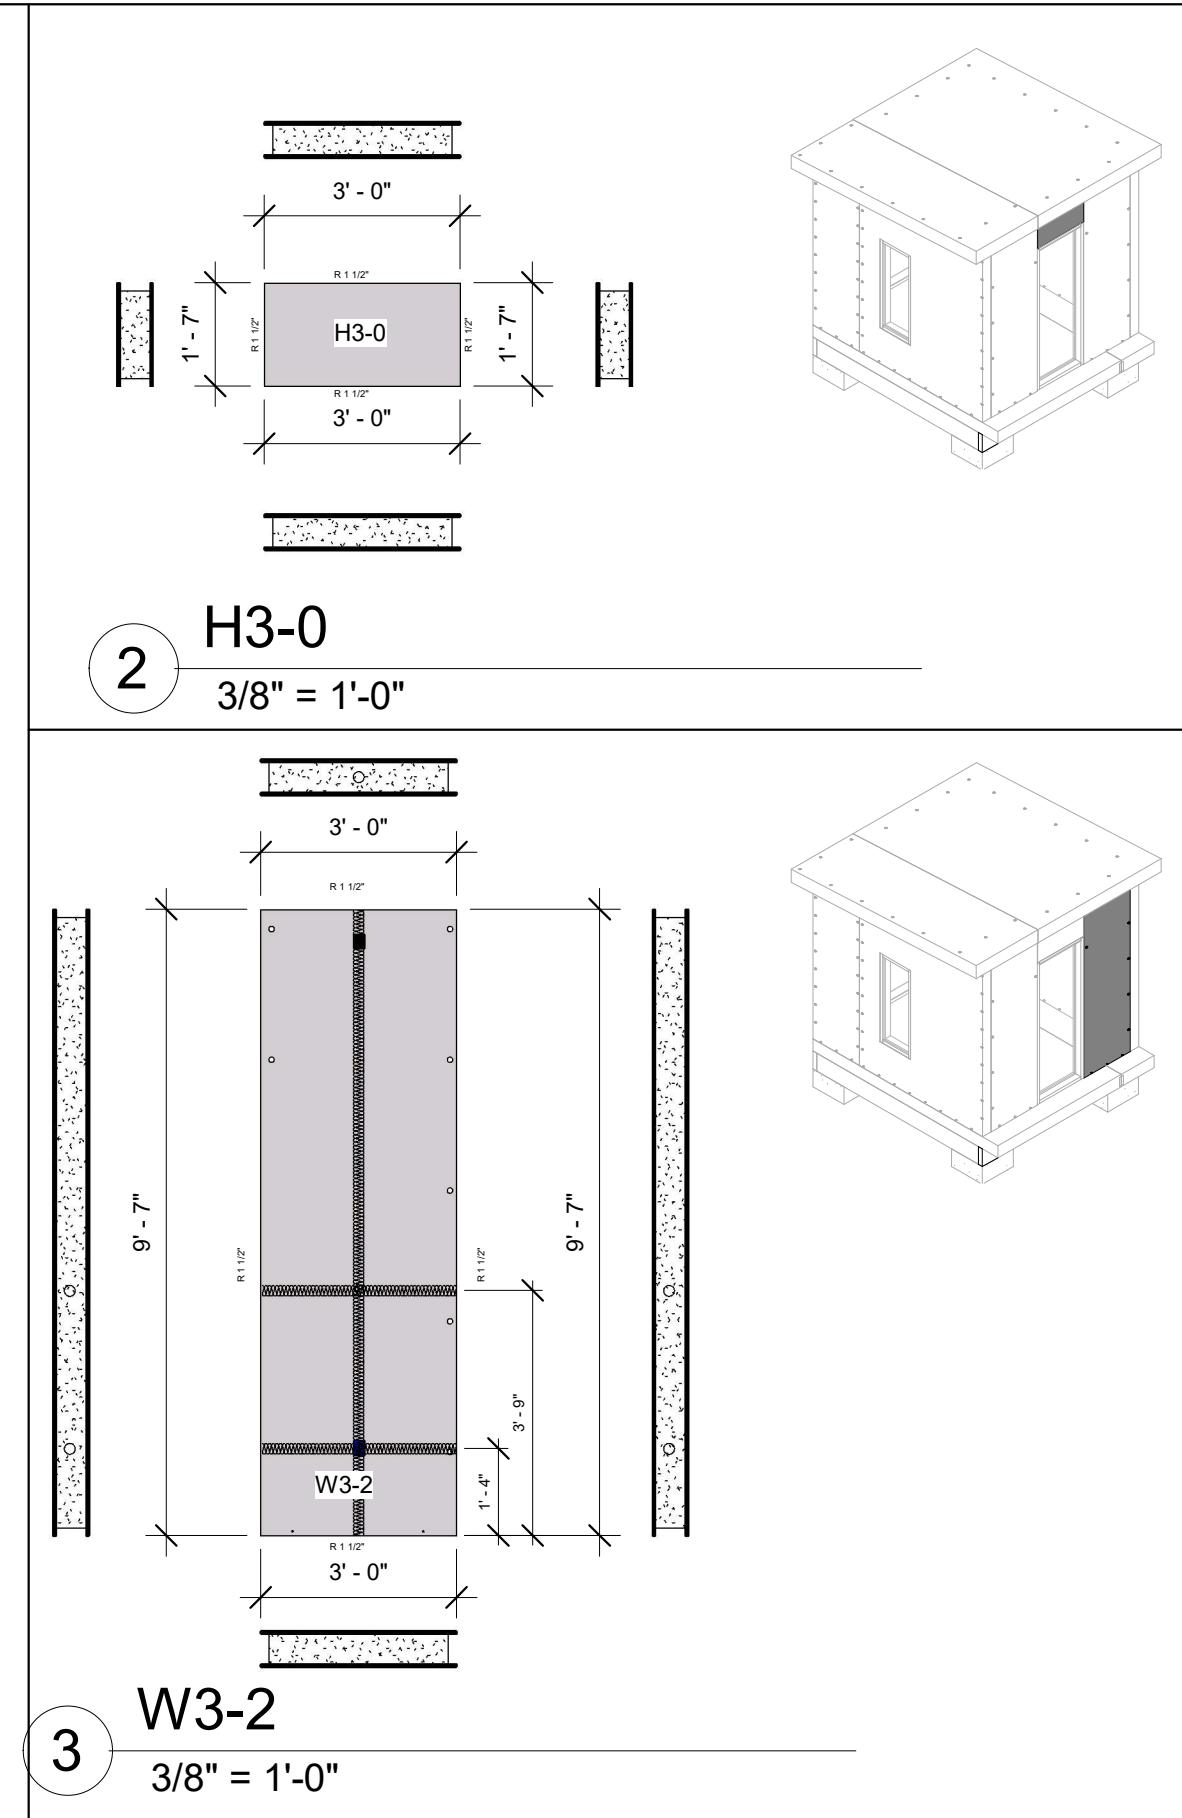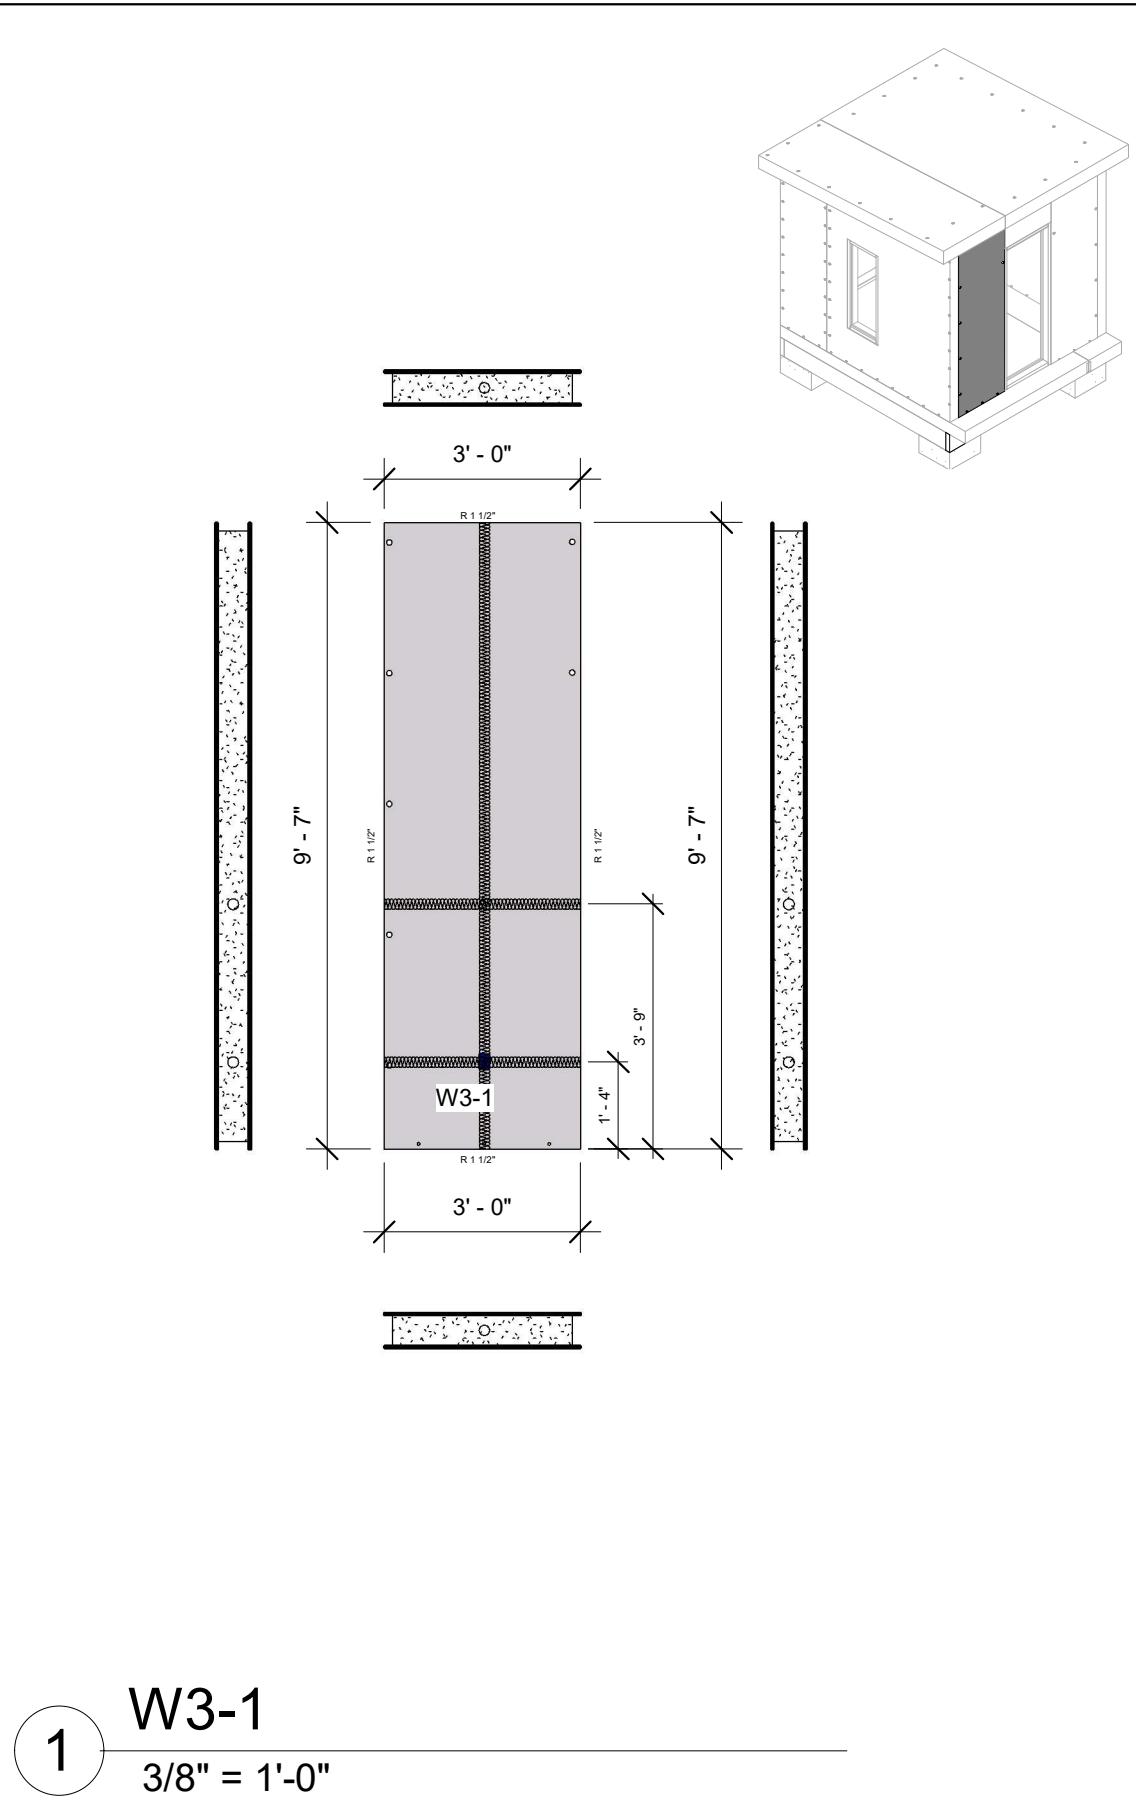

PREFLEX building  
MINI CABIN  
PREFLEX OFFICE

No.	Description	Date



**Shop Drawing  
W3-1,H3-0,W3-2**

Project number	001
Date	Issue Date
Drawn by	Author
Checked by	Checker
A127	
Scale	3/8" = 1'-0"

08/06/2021 08:27:07 a.m.

1 W4-1


3/8" = 1'-0"

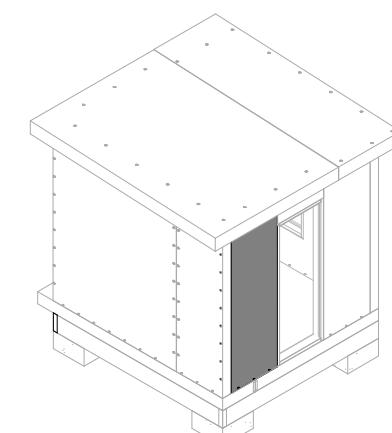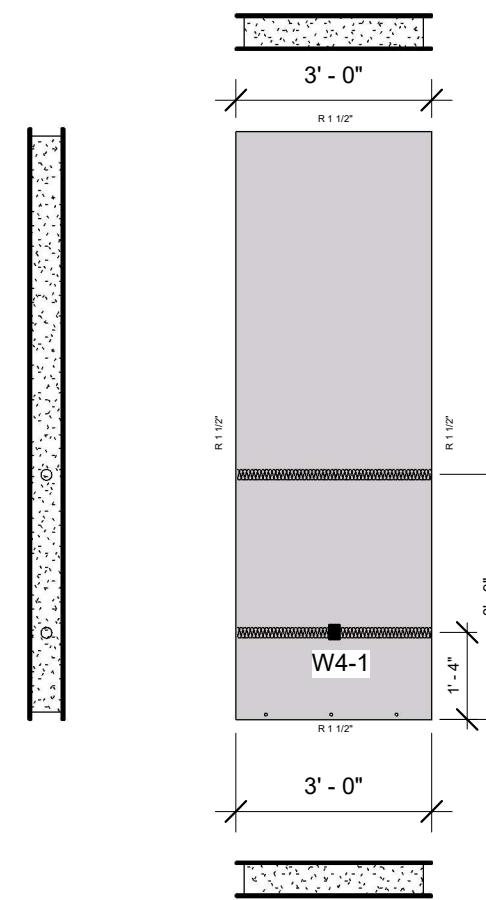

3




W4-2

3/8" = 1'-0"

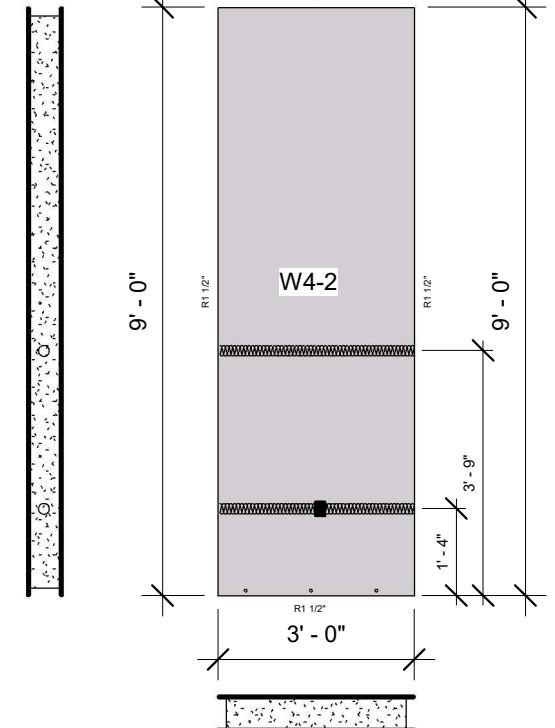

2 H4-0

3/8" = 1'-0"

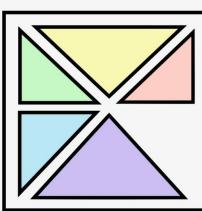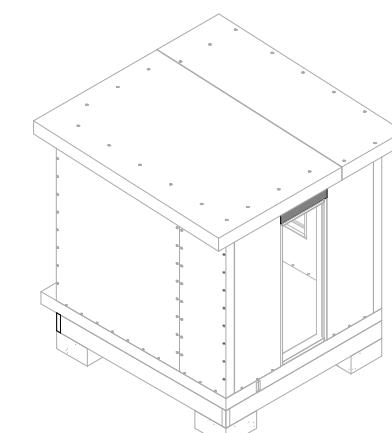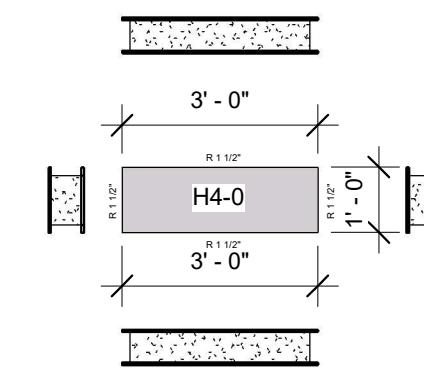

P R E F L E X  
b u i l d i n g

## MINI CABIN



P R E F L E X O F F I C E

No.	Description	Date

## Shop Drawings W4-1, H4-0, W4-2

Project number 001


Date Issue Date

Drawn by Author

Checked by Checker

A128

Scale 3/8" = 1'-0"

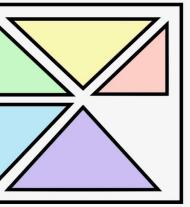

P R E F L E X  
b u i l d i n g

## MINI CABIN



P R E F L E X O F F I C E

No.	Description	Date

## Shop Drawings F1-1, F1-2

Project number 001

Date Issue Date


Drawn by Author

Checked by Checker

A129


Scale 3/8" = 1'-0"

08/06/2021 08:27:10 a.m.

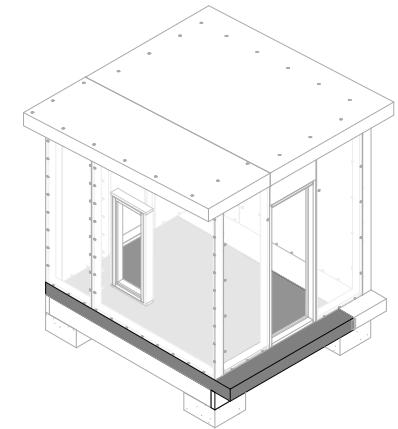



1  
F1-1

3/8" = 1'-0"

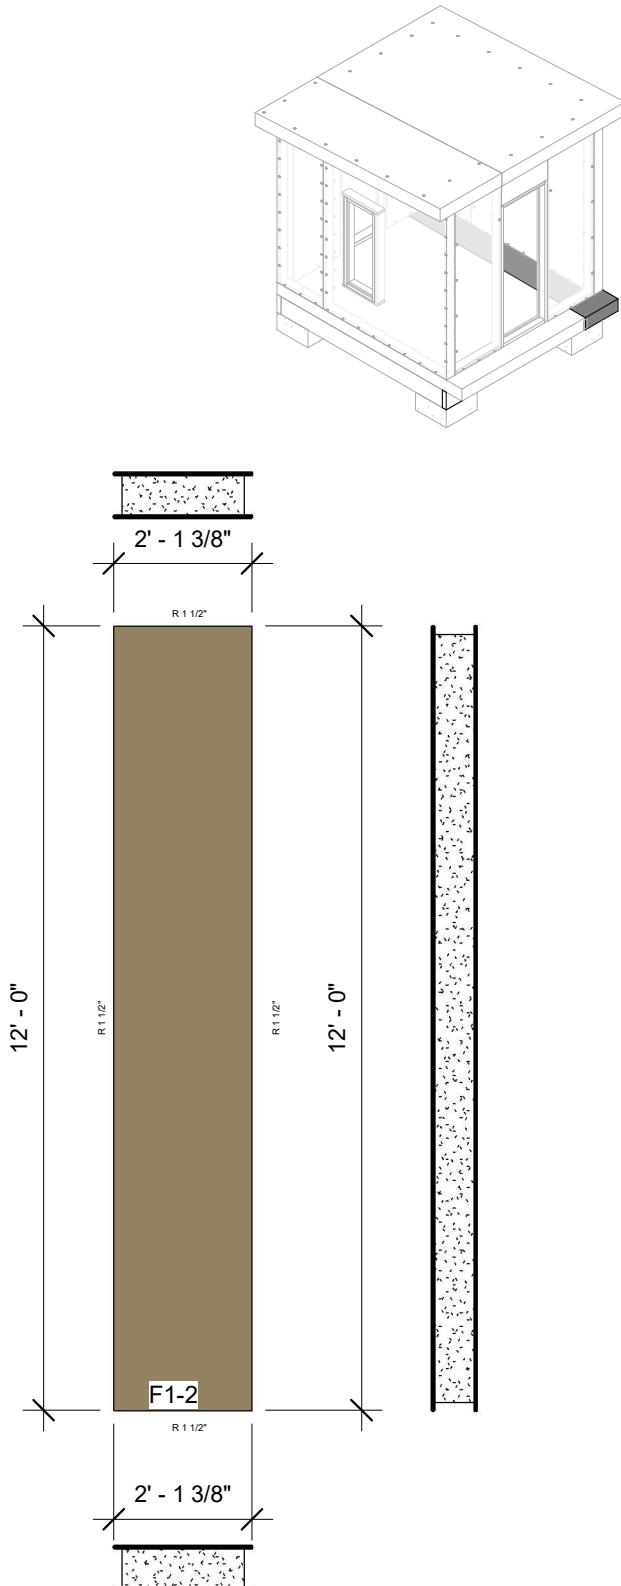

2  
F1-2  
3/8" = 1'-0"

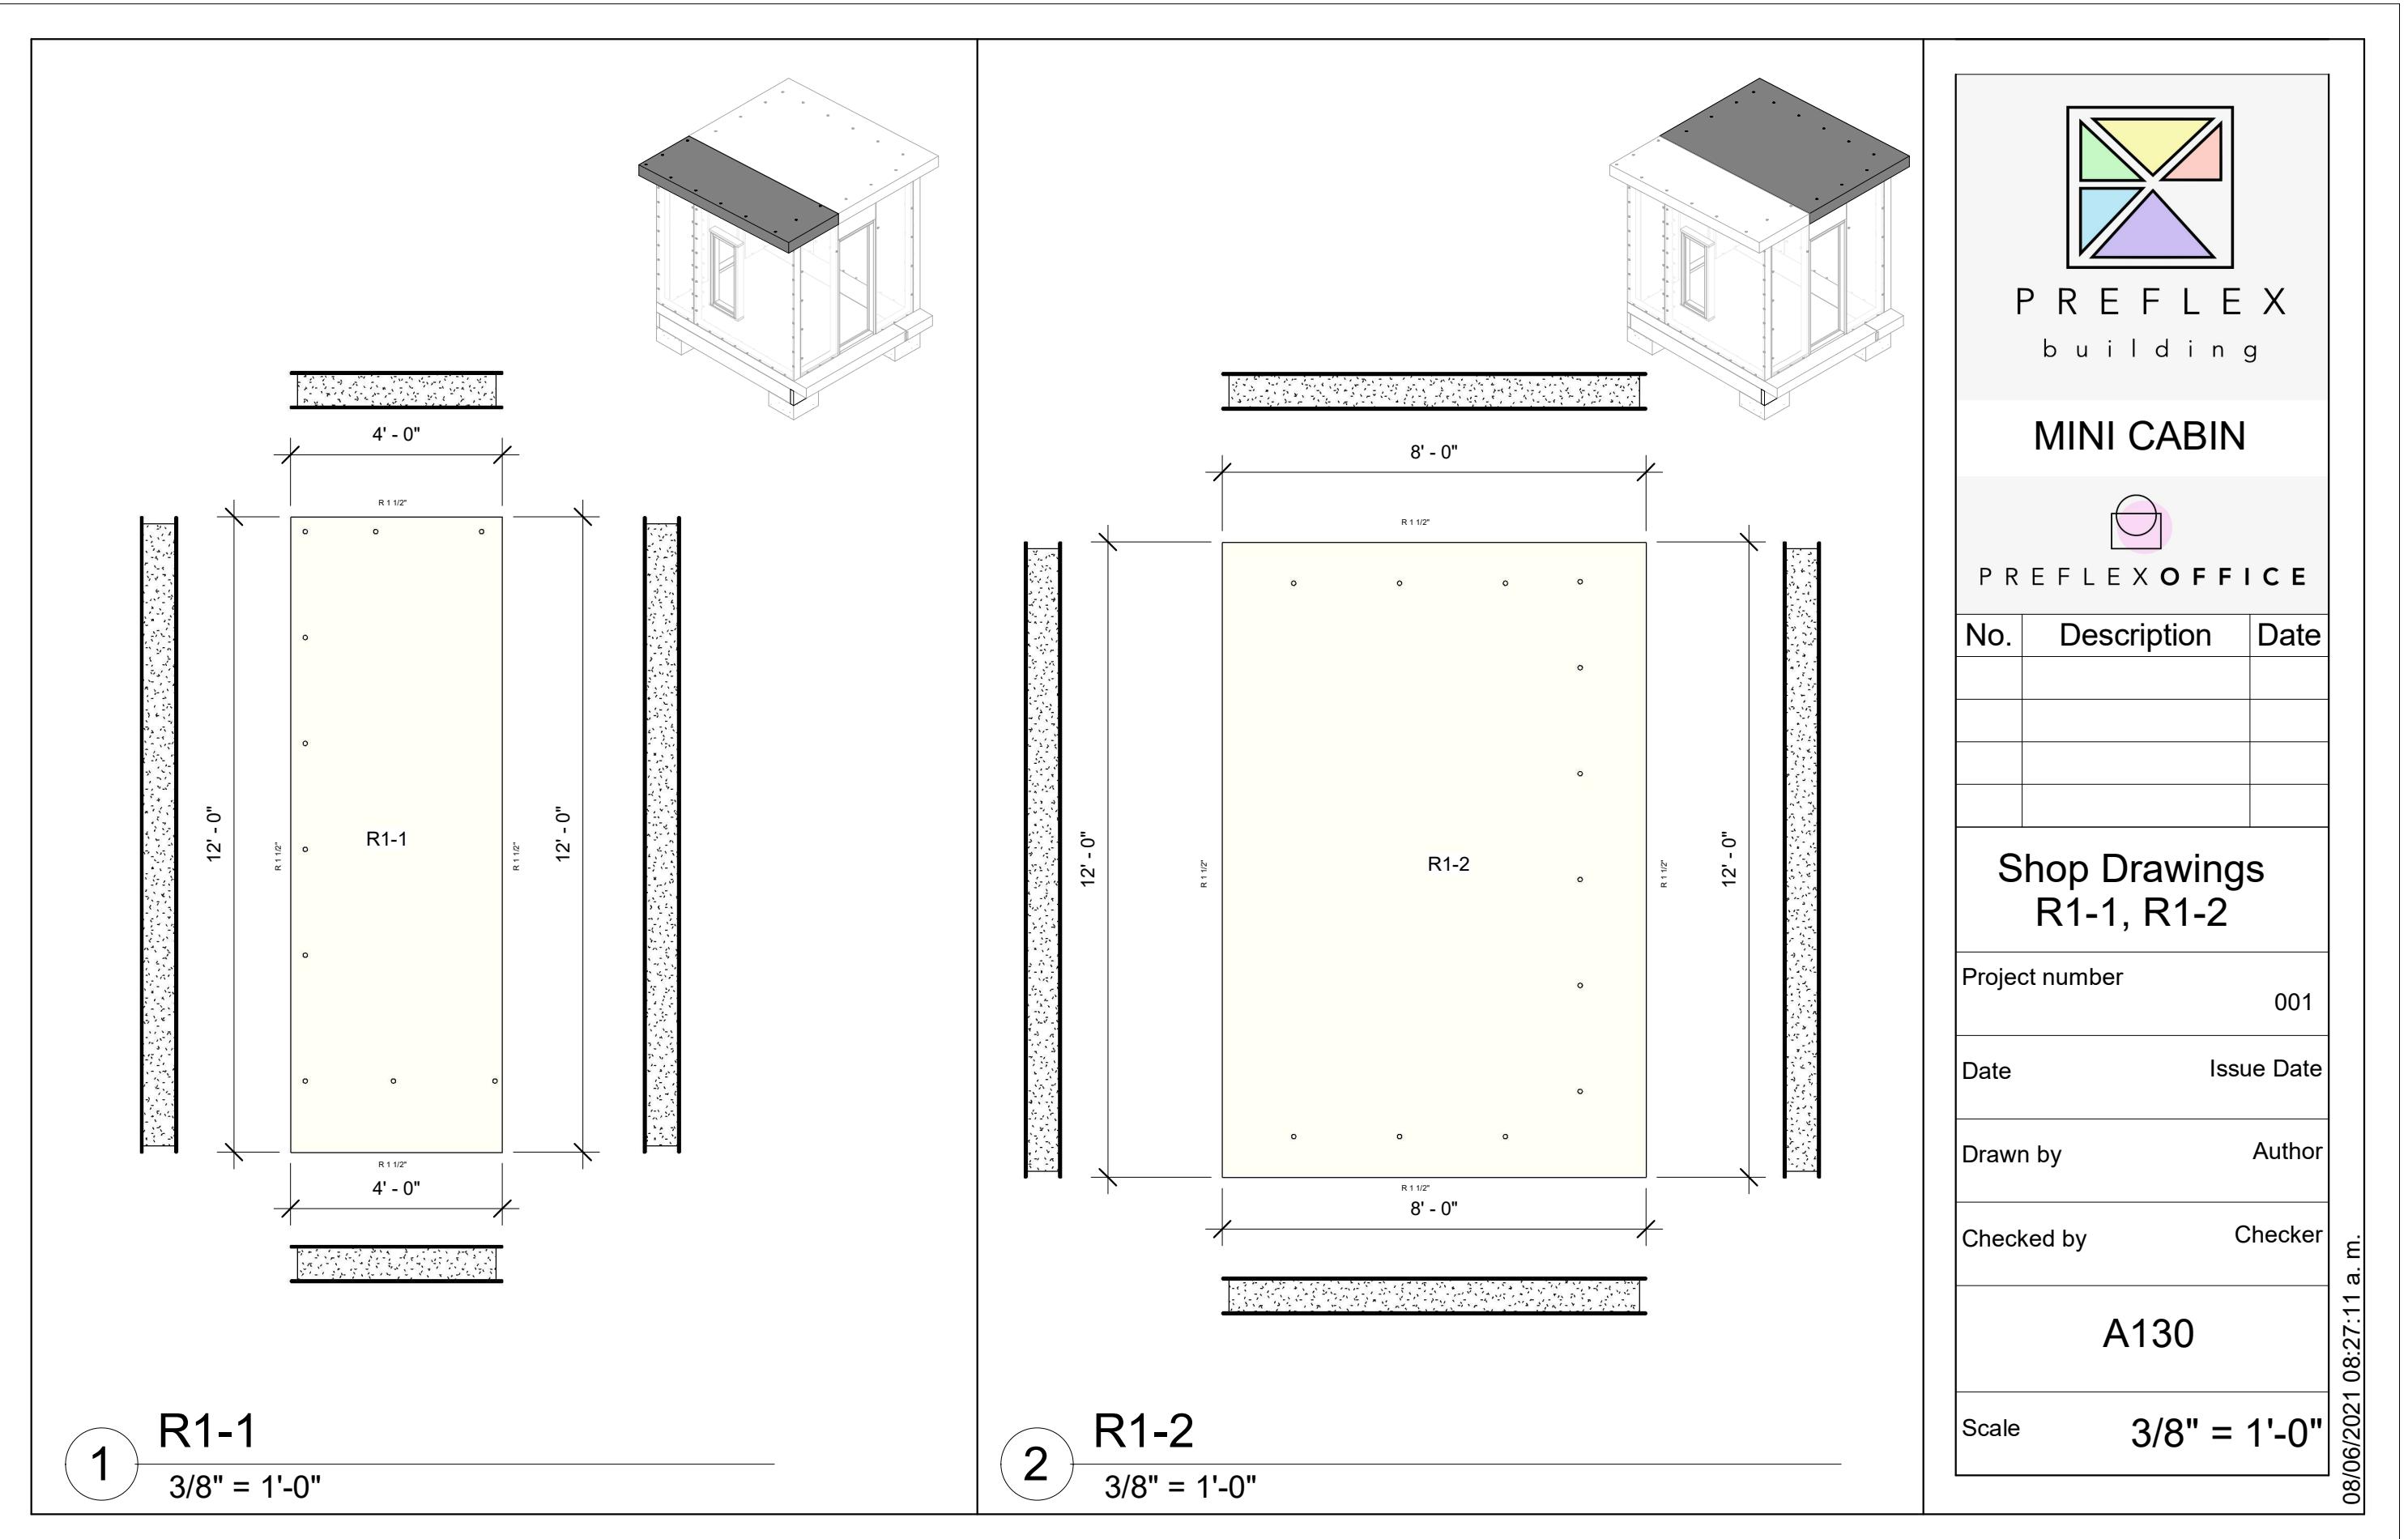

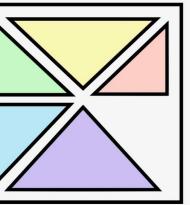

P R E F L E X  
b u i l d i n g

## MINI CABIN







P R E F L E X O F F I C E


No.	Description	Date

## Interior Views

Project number	001
Date	Issue Date
Drawn by	Author
Checked by	Checker
A131	
Scale	1/4" = 1'-0"

08/06/2021 08:27:12 a.m.

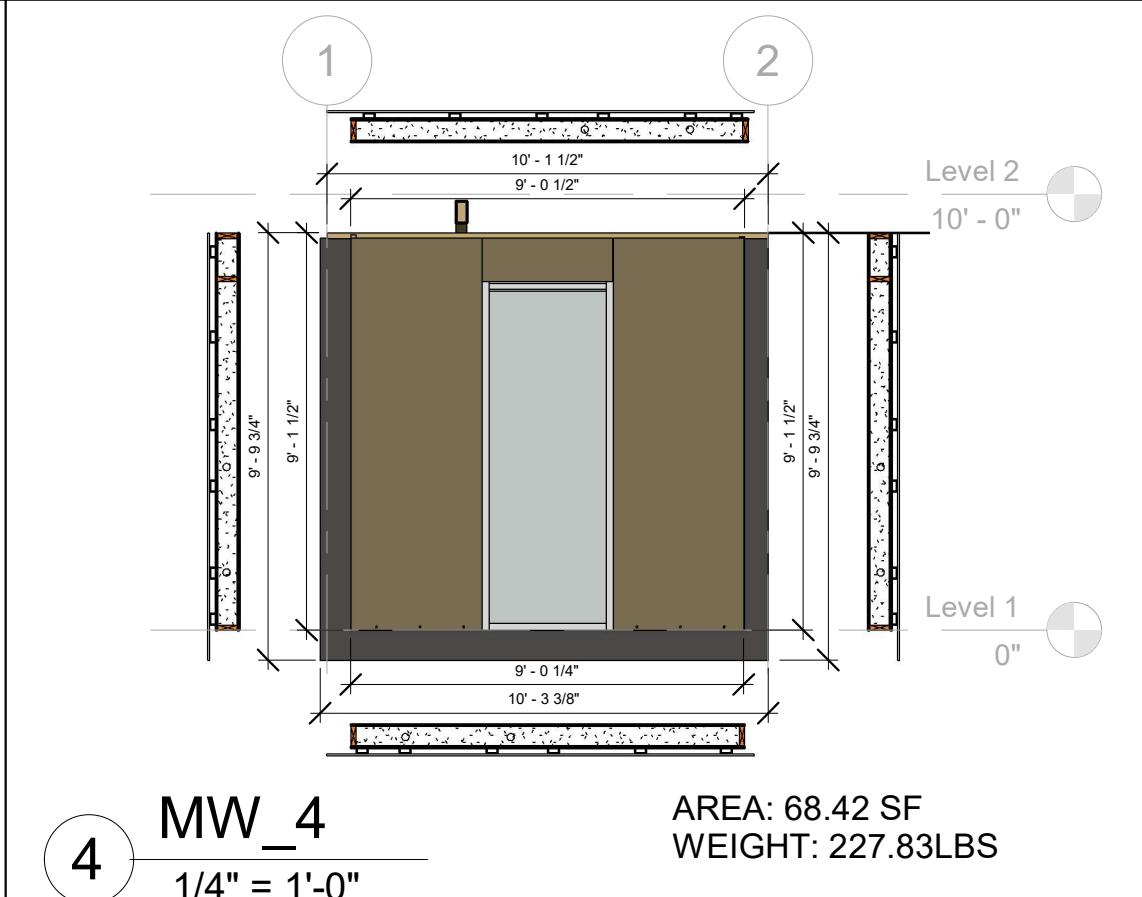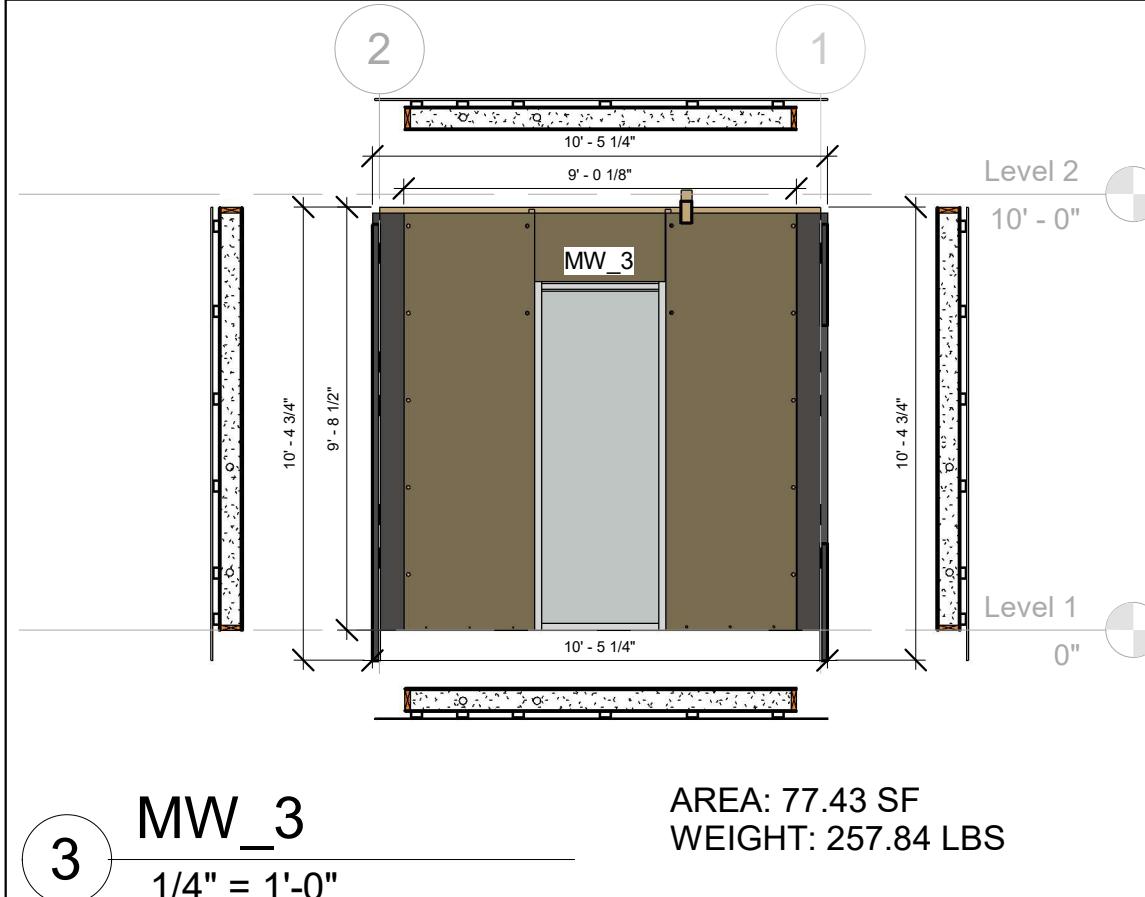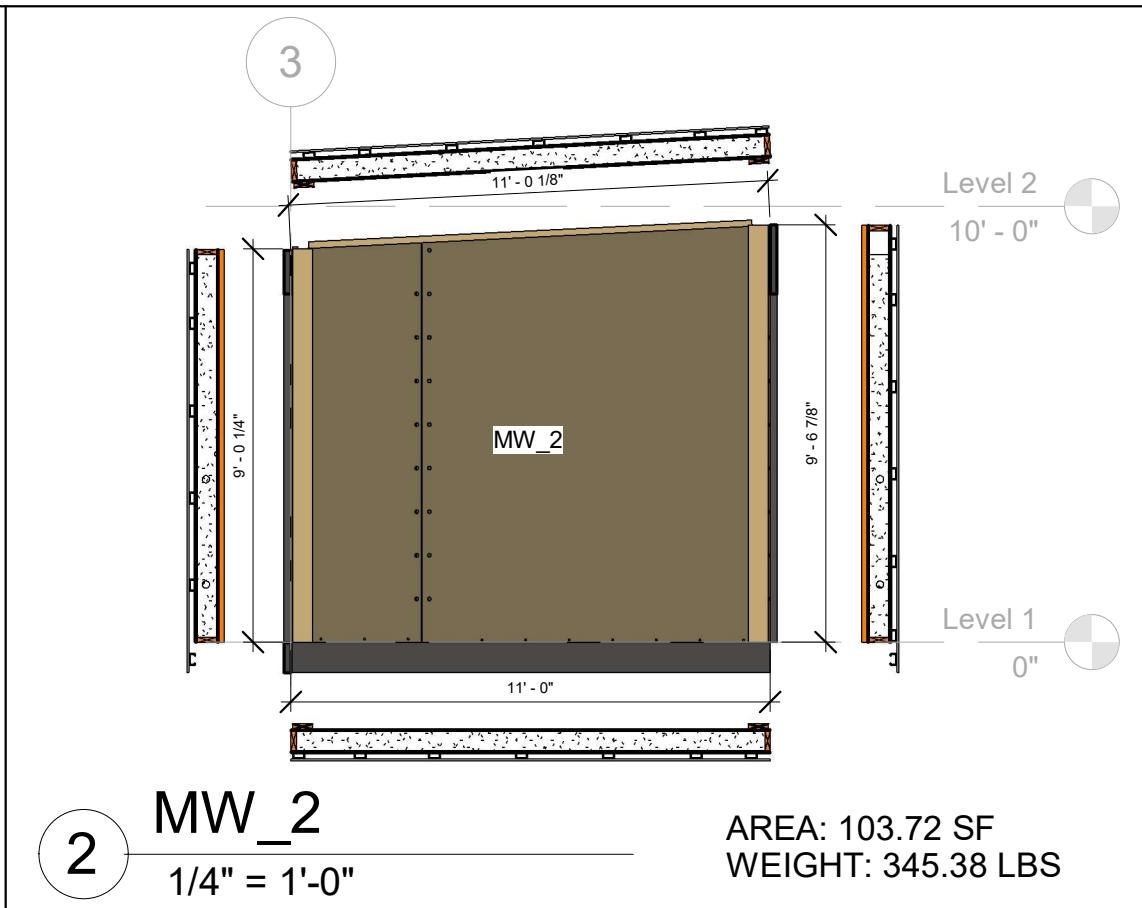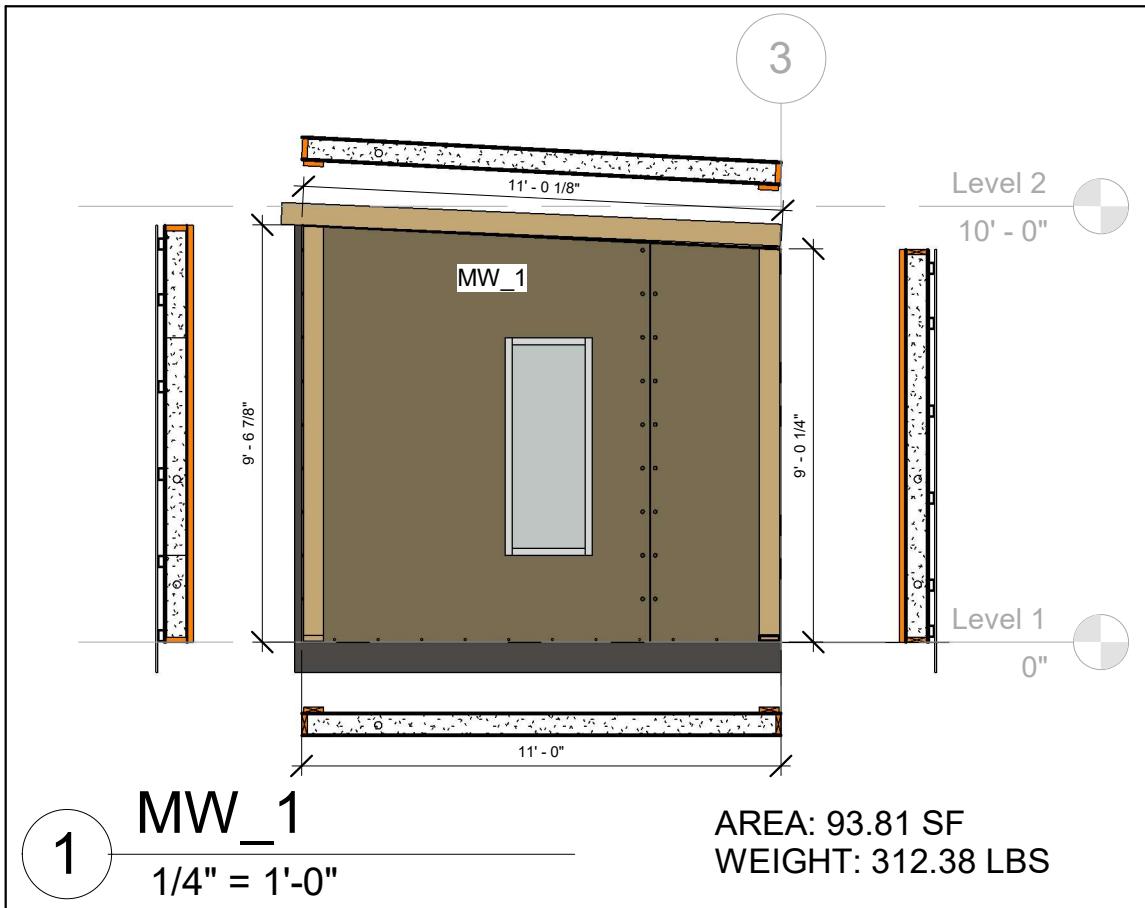

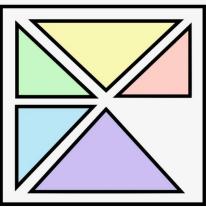

P R E F L E X  
b u i l d i n g

## MINI CABIN



P R E F L E X O F F I C E

No.	Description	Date
1	Revision 1	Date 1

## Packing to Transport

Project number 001

Date Issue Date


Drawn by Author

Checked by Checker


A132

Scale

08/06/2021 08:27:14 a. m.

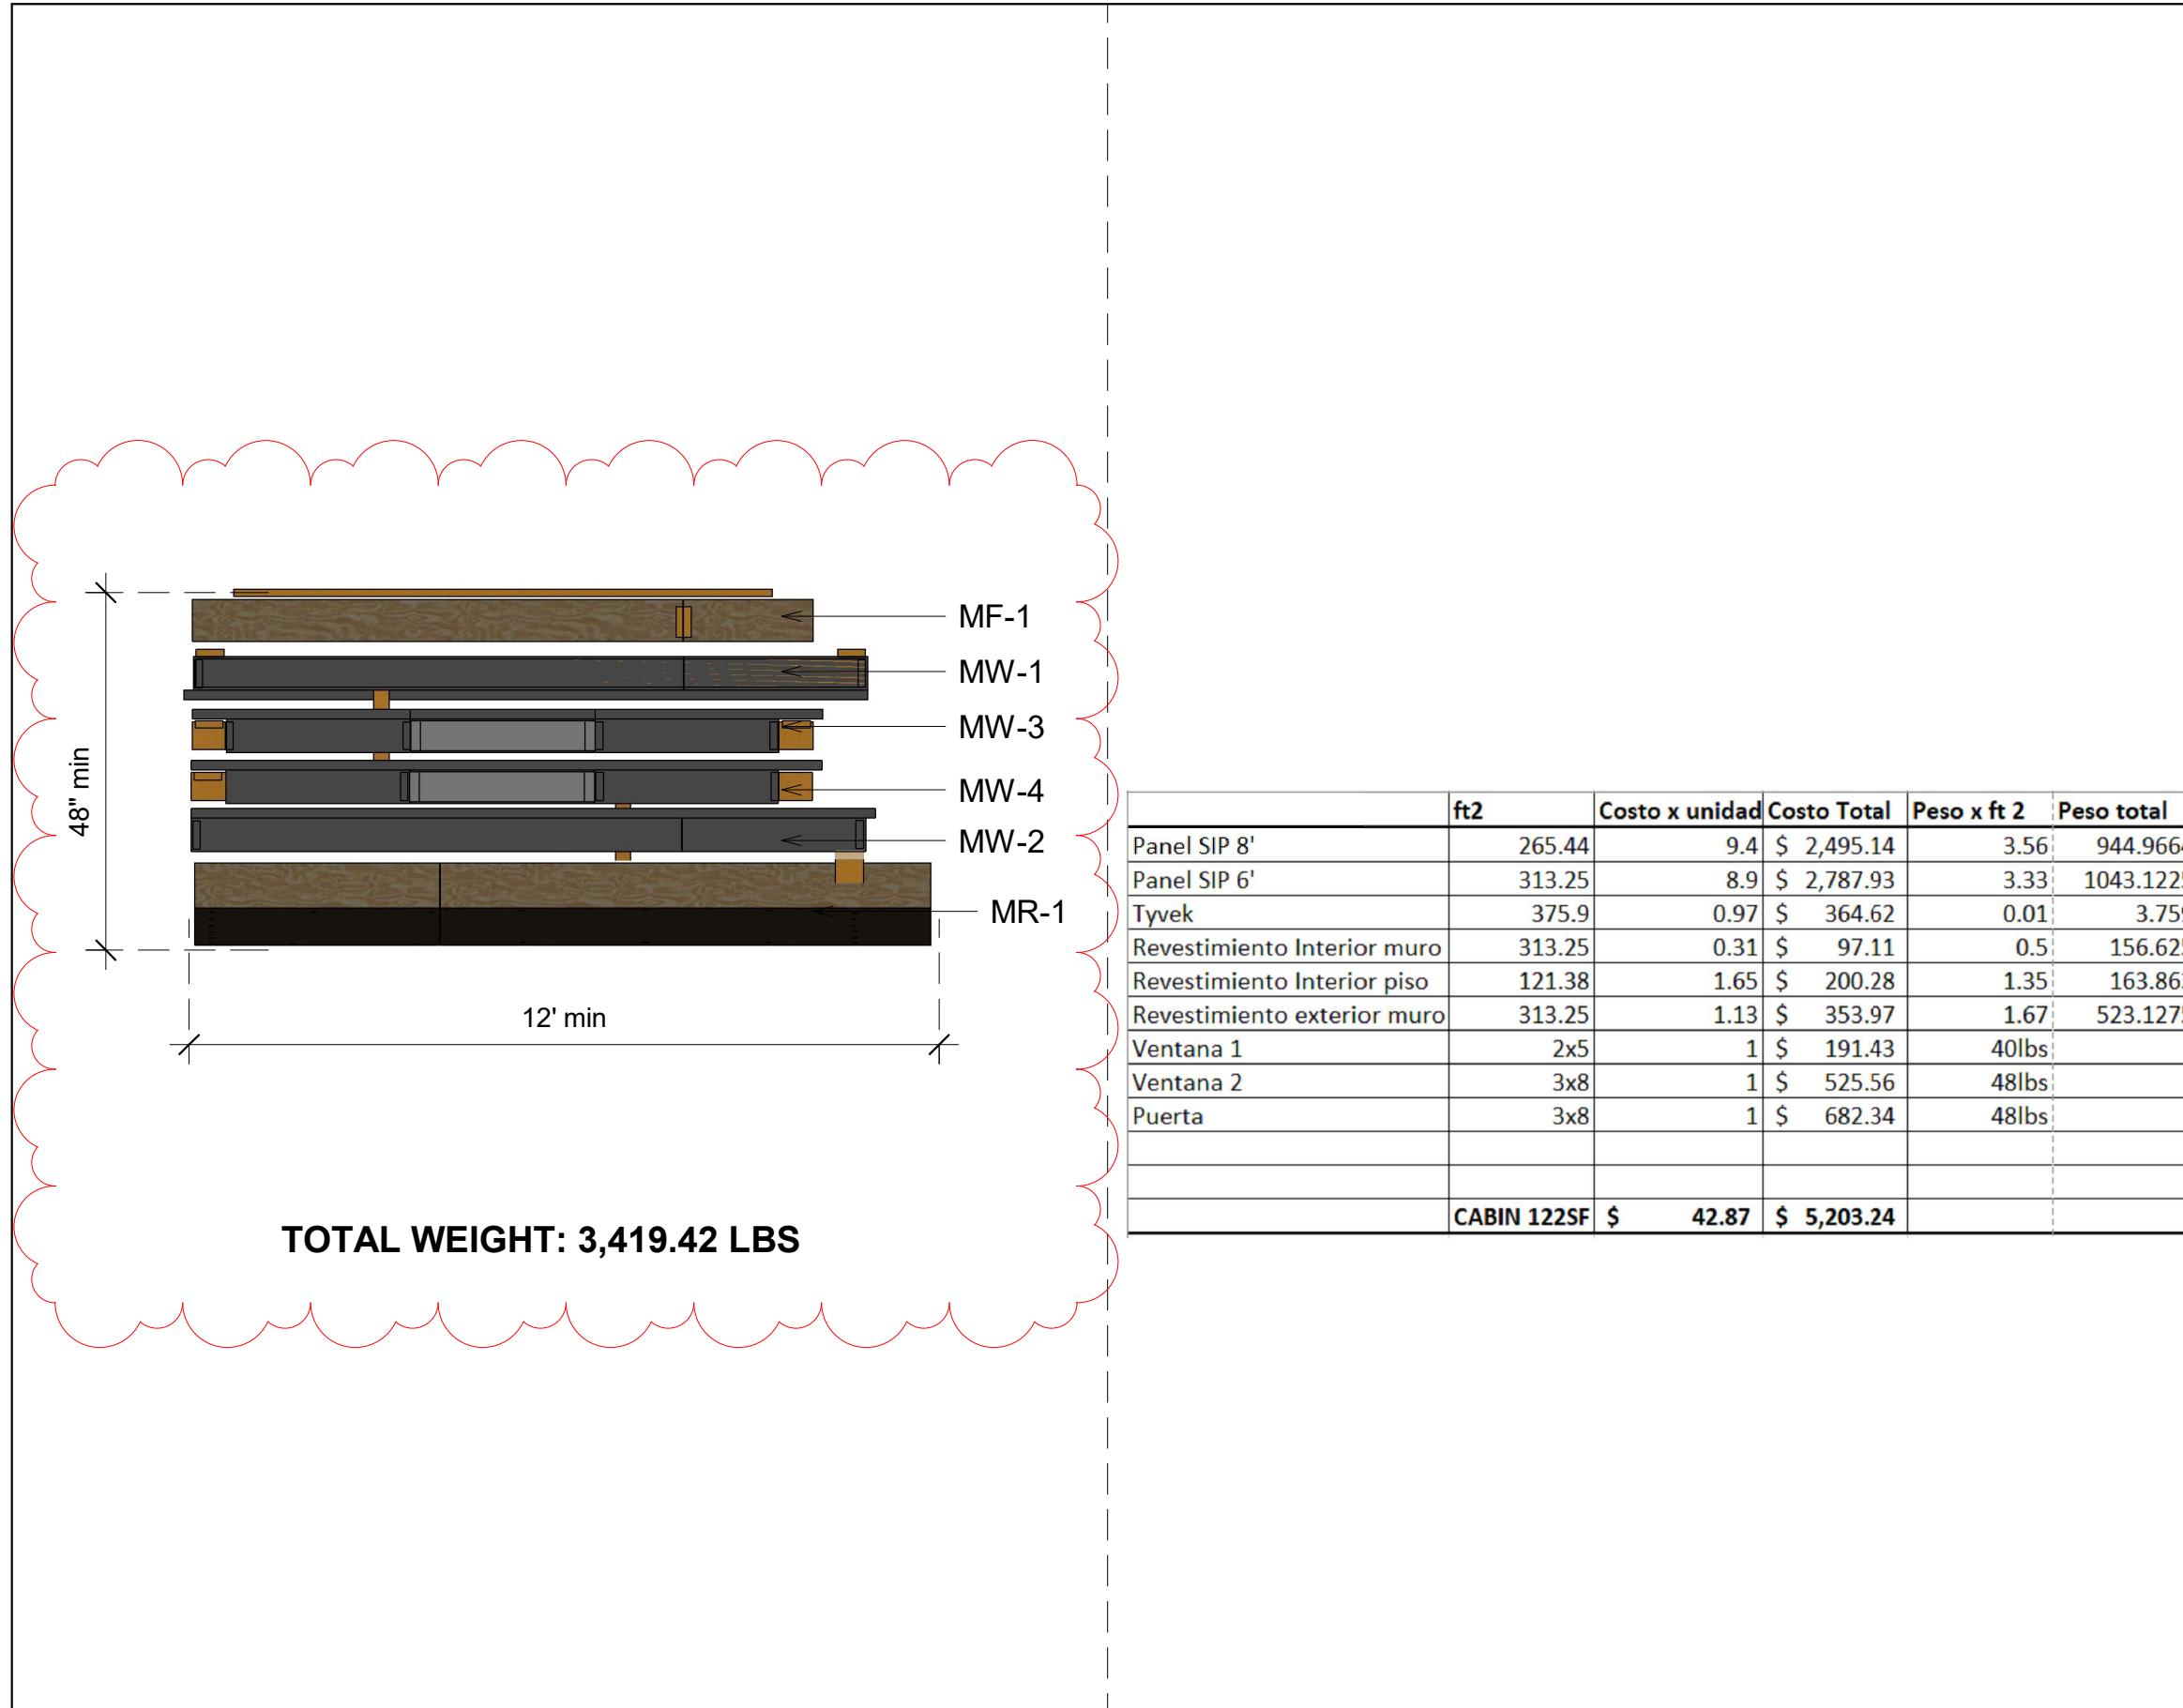

<b>HIGH PART OF TRANSPORT</b>				
		MF-1	AREA: 121.38 SF WEIGHT SPI: 432.00 LBS FINISHES WEIGHT: 163.86 LBS  TOTAL WEIGHT: 595.86 LBS	
		MW-1	AREA: 93.81 SF WEIGHT: 312.38 LBS FINISHES WEIGHT: 245.00 LBS  TOTAL WEIGHT: 557.38 LBS	
		MW-3	AREA: 77.43 SF WEIGHT: 257.84 LBS FINISHES WEIGHT: 210.60LBS  TOTAL WEIGHT: 468.44 LBS	
		MW-4	AREA: 68.42 SF WEIGHT: 227.83LBS FINISHES WEIGHT: 191.68LBS  TOTAL WEIGHT: 419.51 LBS	
		MW-2	AREA: 103.72 SF WEIGHT: 345.38 LBS FINISHES WEIGHT: 217.81LBS  TOTAL WEIGHT: 563.19 LBS	
		MR-1	AREA: 144 SF WEIGHT: 512.64 LBS FINISHES WEIGHT: 302.40LBS  TOTAL WEIGHT: 815.04 LBS	<b>TOTAL WEIGHT: 3,419.42 LBS</b>
<b>BOTTOM OF TRANSPORT</b>				

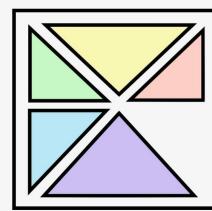

P R E F L E X  
b u i l d i n g

MINI CABIN



P R E F L E X O F F I C E

No.	Description	Date

Tidy Packing

Project number 001

Date Issue Date

Drawn by Author

Checked by Checker

A133

Scale